



BANGUNAN KOMERSIAL

LOKASI

Kendari, Sulawesi Tenggara

DI GAMBAR OLEH

PARAF

ATIKA, S.Ars

PEMILIK PROYEK

PARAF

AZAM

NAMA GAMBAR

GARIS SEMPADAN JALAN

1.
2.
3.
4.

SKALA

NO. LEMBAR



TAMPAK DEPAN

NON SKALA



BANGUNAN KOMERSIAL

LOKASI

Kendari, Sulawesi Tenggara

DI GAMBAR OLEH

PARAF

ATIKA, S.Ars

PEMILIK PROYEK

PARAF

AZAM

NAMA GAMBAR

GARIS SEMPADAN JALAN

- 1.
- 2.
- 3.
- 4.

SKALA

NO. LEMBAR



TAMPAK SAMPING KIRI
NON SKALA



BANGUNAN KOMERSIAL

LOKASI

Kendari, Sulawesi Tenggara

DI GAMBAR OLEH

PARAF

ATIKA, S.Ars

PEMILIK PROYEK

PARAF

AZAM

NAMA GAMBAR

GARIS SEMPADAN JALAN

- 1.
- 2.
- 3.
- 4.

SKALA

NO. LEMBAR



TAMPAK BELAKANG
NON SKALA



BANGUNAN KOMERSIAL

LOKASI

Kendari, Sulawesi Tenggara

DI GAMBAR OLEH

PARAF

ATIKA, S.Ars

PEMILIK PROYEK

PARAF

AZAM

NAMA GAMBAR


GARIS SEMPADAN JALAN

- 1.
- 2.
- 3.
- 4.

SKALA

NO. LEMBAR

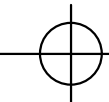

 **TAMPAK SAMPING KANAN**
NON SKALA



BANGUNAN KOMERSIAL

LOKASI

Kendari, Sulawesi Tenggara

DI GAMBAR OLEH

PARAF

ATIKA, S.Ars

PEMILIK PROYEK

PARAF

AZAM


NAMA GAMBAR

GARIS SEMPADAN JALAN


- 1.
- 2.
- 3.
- 4.

SKALA

NO. LEMBAR

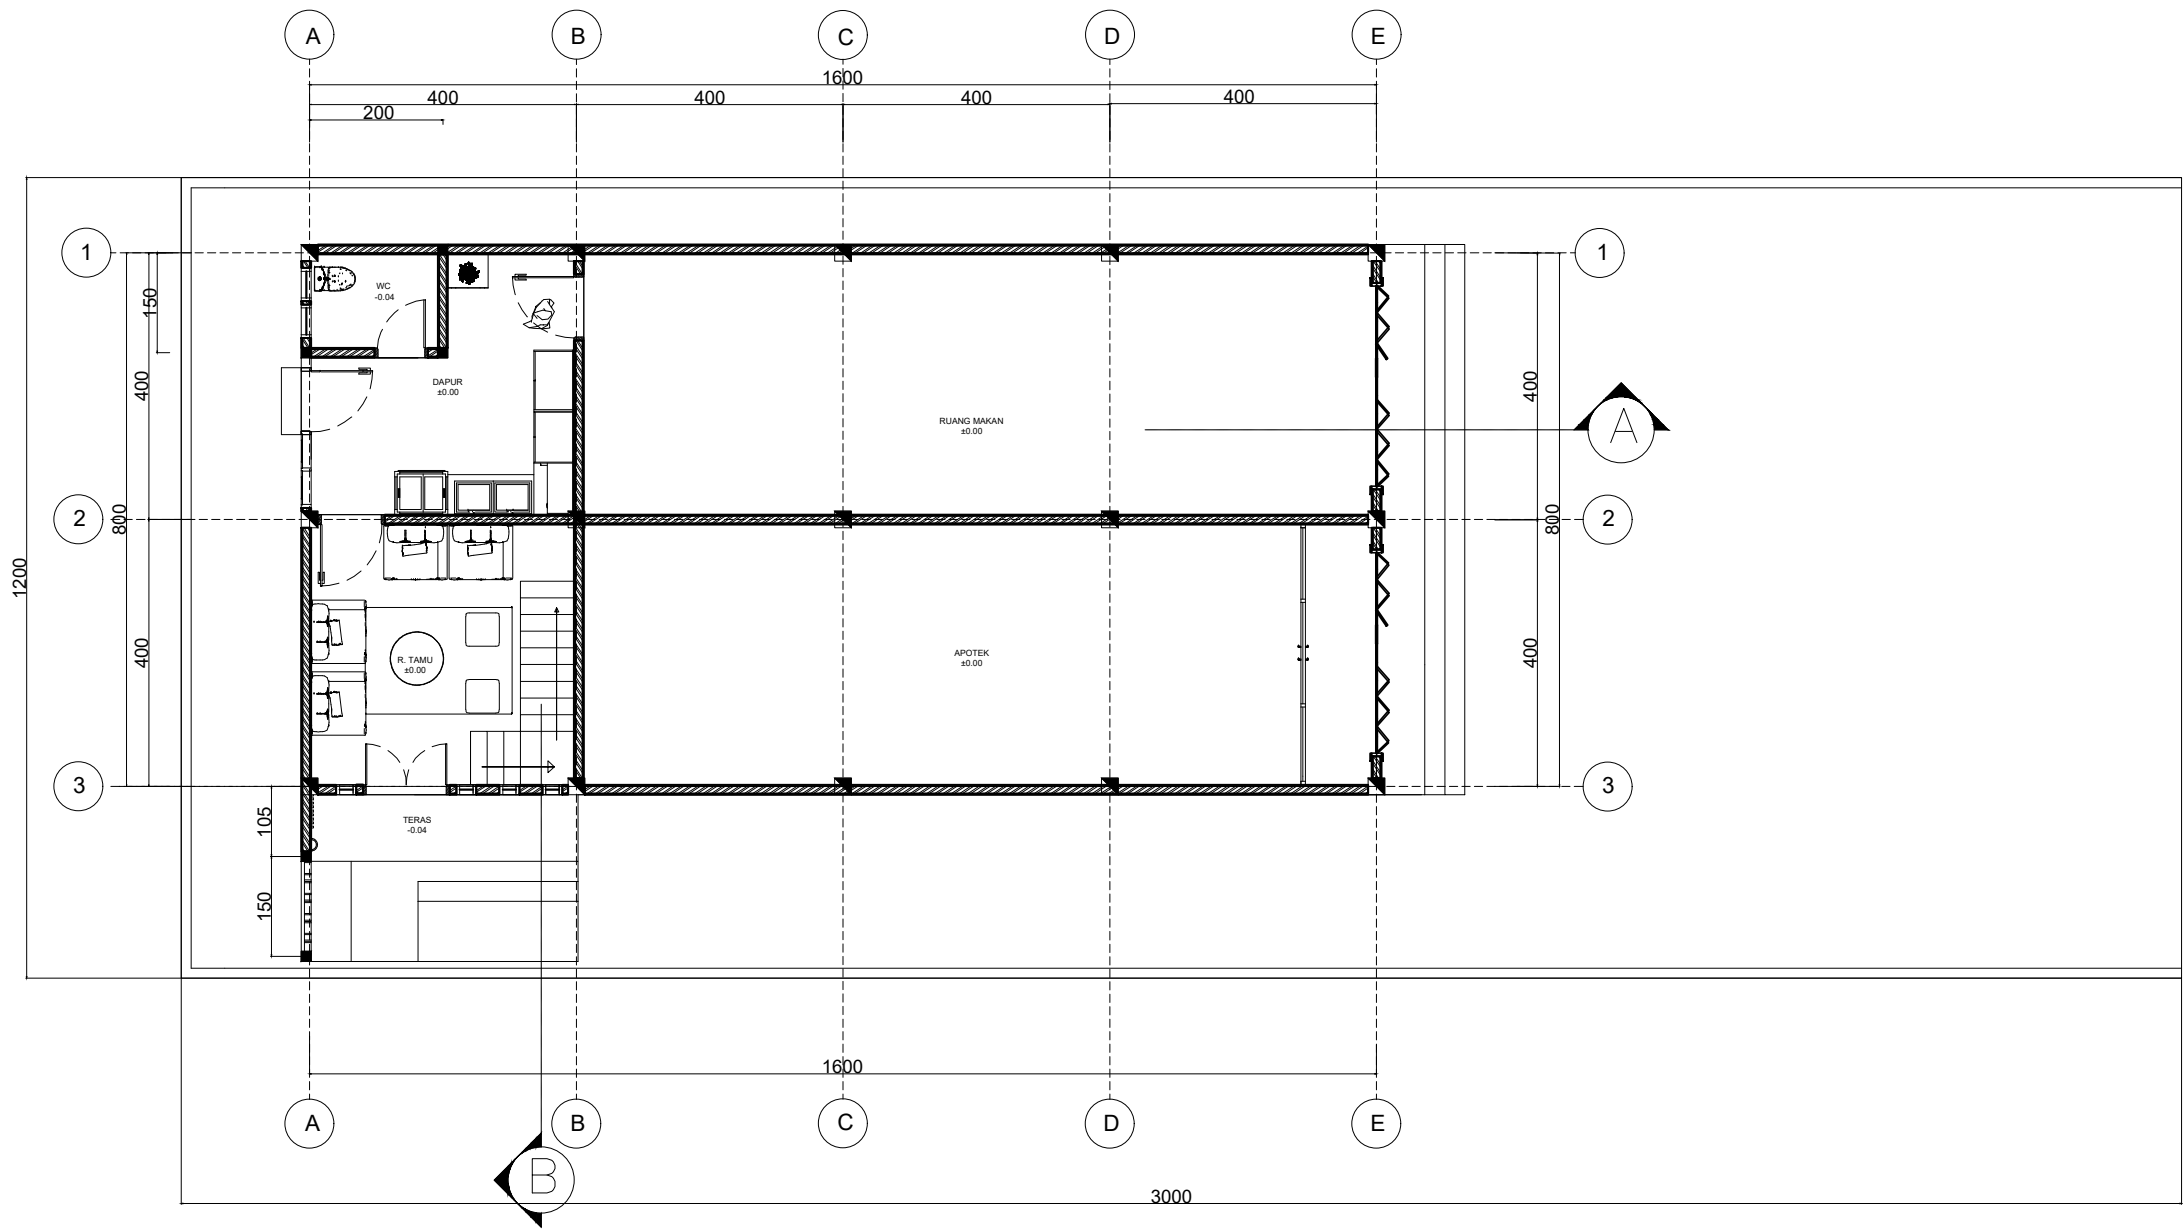


DENAH LT 1
SKALA 1:100

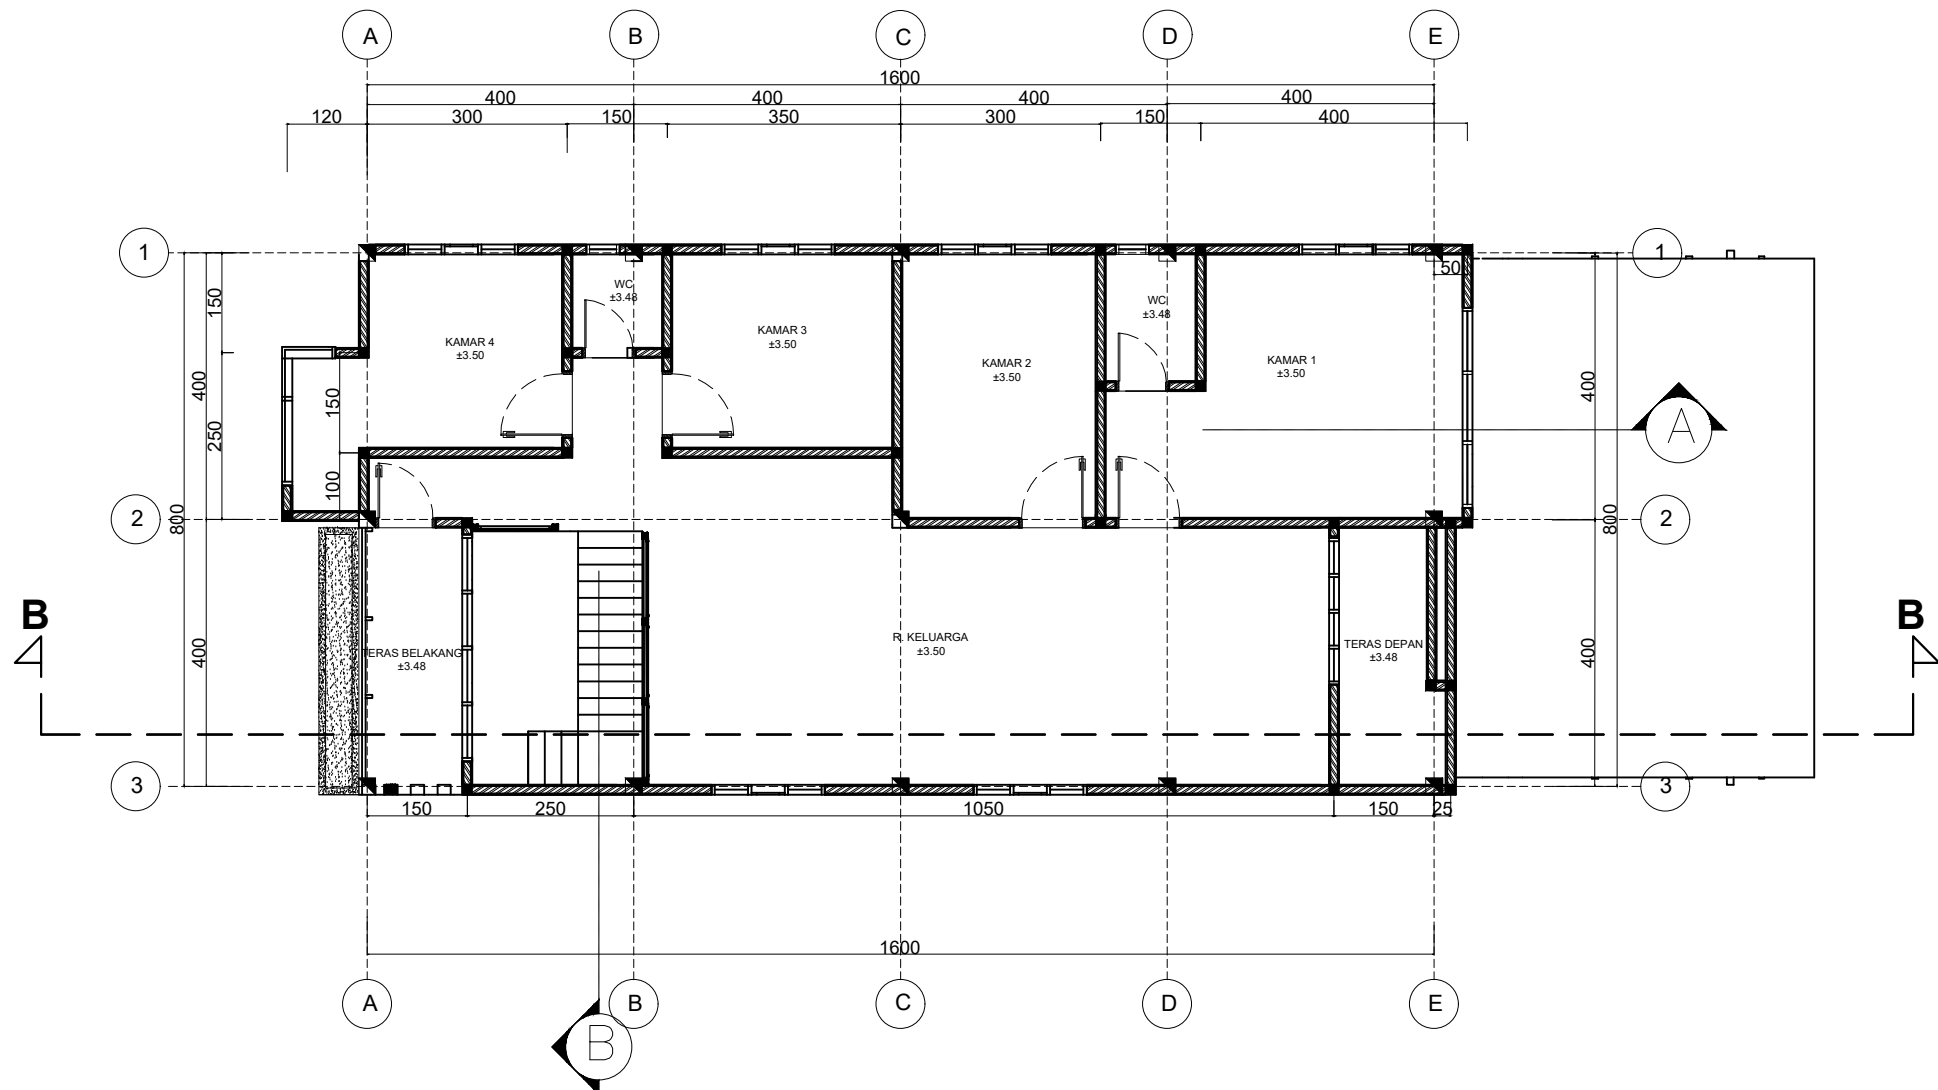

DENAH LT 2
SKALA 1:100



BANGUNAN KOMERSIAL	
LOKASI	
Kendari, Sulawesi Tenggara	
DI GAMBAR OLEH	PARAF
ATIKA, S.Ars	
PEMILIK PROYEK	PARAF
AZAM	
NAMA GAMBAR	
GARIS SEMPADAN JALAN	
1.	
2.	
3.	
4.	
SKALA	NO. LEMBAR

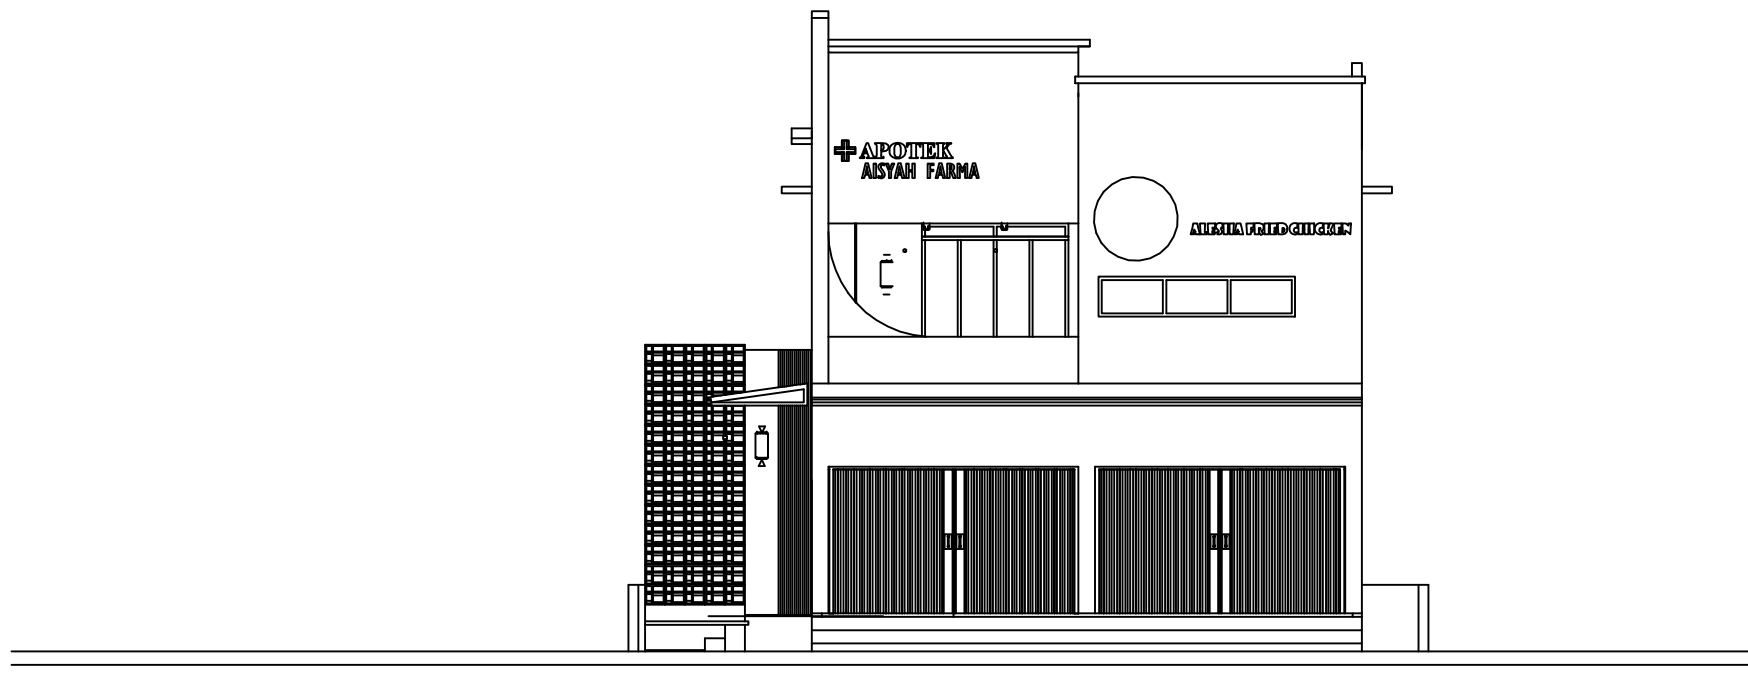


RENCANA PONDASI POER PLAT
SKALA 1:100



BANGUNAN KOMERSIAL	
LOKASI	
Kendari, Sulawesi Tenggara	
DI GAMBAR OLEH	PARAF
ATIKA, S.Ars	
PEMILIK PROYEK	PARAF
AZAM	
NAMA GAMBAR	
GARIS SEMPADAN JALAN	
1.	
2.	
3.	
4.	
SKALA	NO. LEMBAR

	
BANGUNAN KOMERSIAL	
LOKASI	
Kendari, Sulawesi Tenggara	
DI GAMBAR OLEH	PARAF
ATIKA, S.Ars	
PEMILIK PROYEK	PARAF
AZAM	
NAMA GAMBAR	
GARIS SEMPADAN JALAN	
1.	
2.	
3.	
4.	
SKALA	NO. LEMBAR

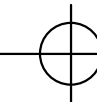

 RENCANA PONDASI POER PLAT
SKALA 1:100



BANGUNAN KOMERSIAL

LOKASI

Kendari, Sulawesi Tenggara

DI GAMBAR OLEH

PARAF

ATIKA, S.Ars

PEMILIK PROYEK

PARAF

AZAM


NAMA GAMBAR


GARIS SEMPADAN JALAN

1.
2.
3.
4.

SKALA

NO. LEMBAR

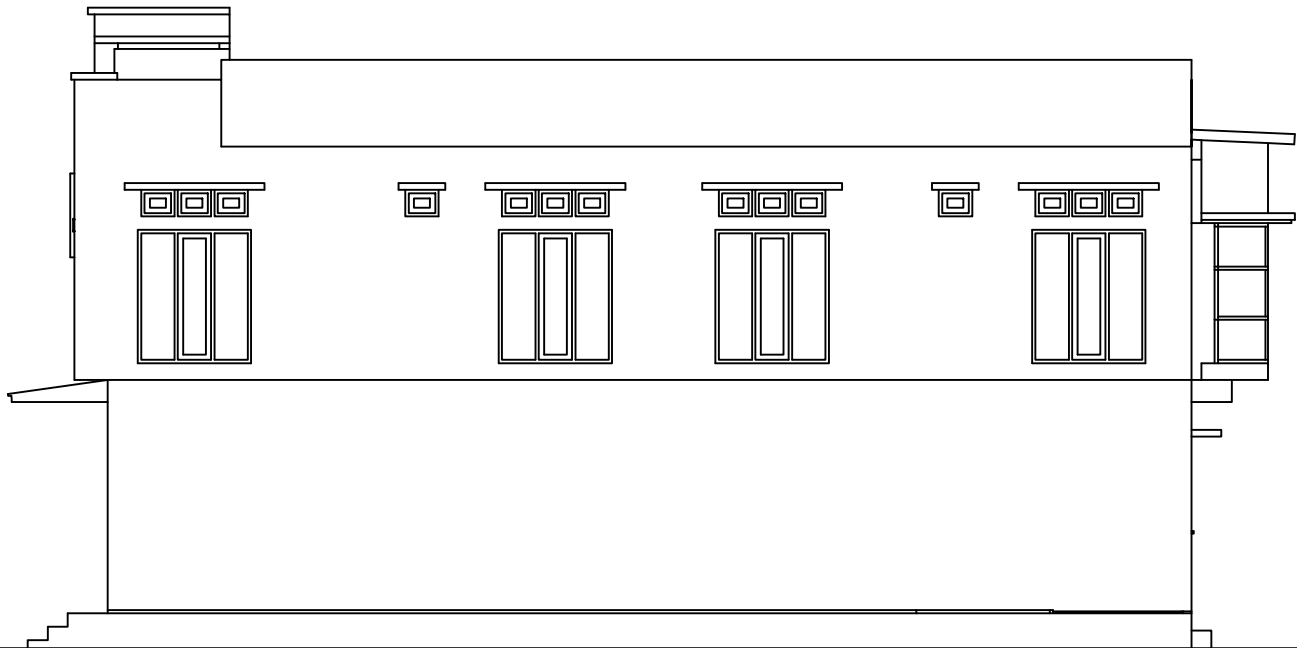

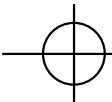RENCANA PONDASI POER PLAT
SKALA 1:100



BANGUNAN KOMERSIAL

LOKASI

Kendari, Sulawesi Tenggara

DI GAMBAR OLEH

PARAF

ATIKA, S.Ars

PEMILIK PROYEK

PARAF

AZAM


NAMA GAMBAR

GARIS SEMPADAN JALAN


- 1.
- 2.
- 3.
- 4.

SKALA

NO. LEMBAR

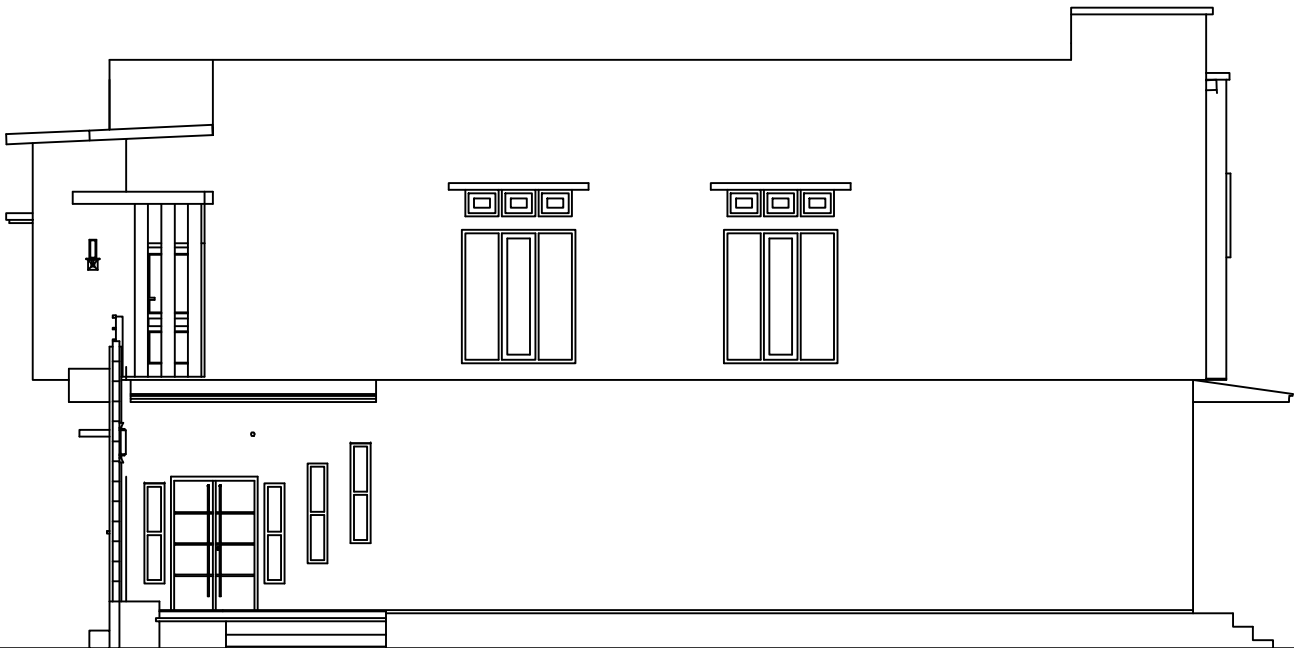

RENCANA PONDASI POER PLAT
SKALA 1:100

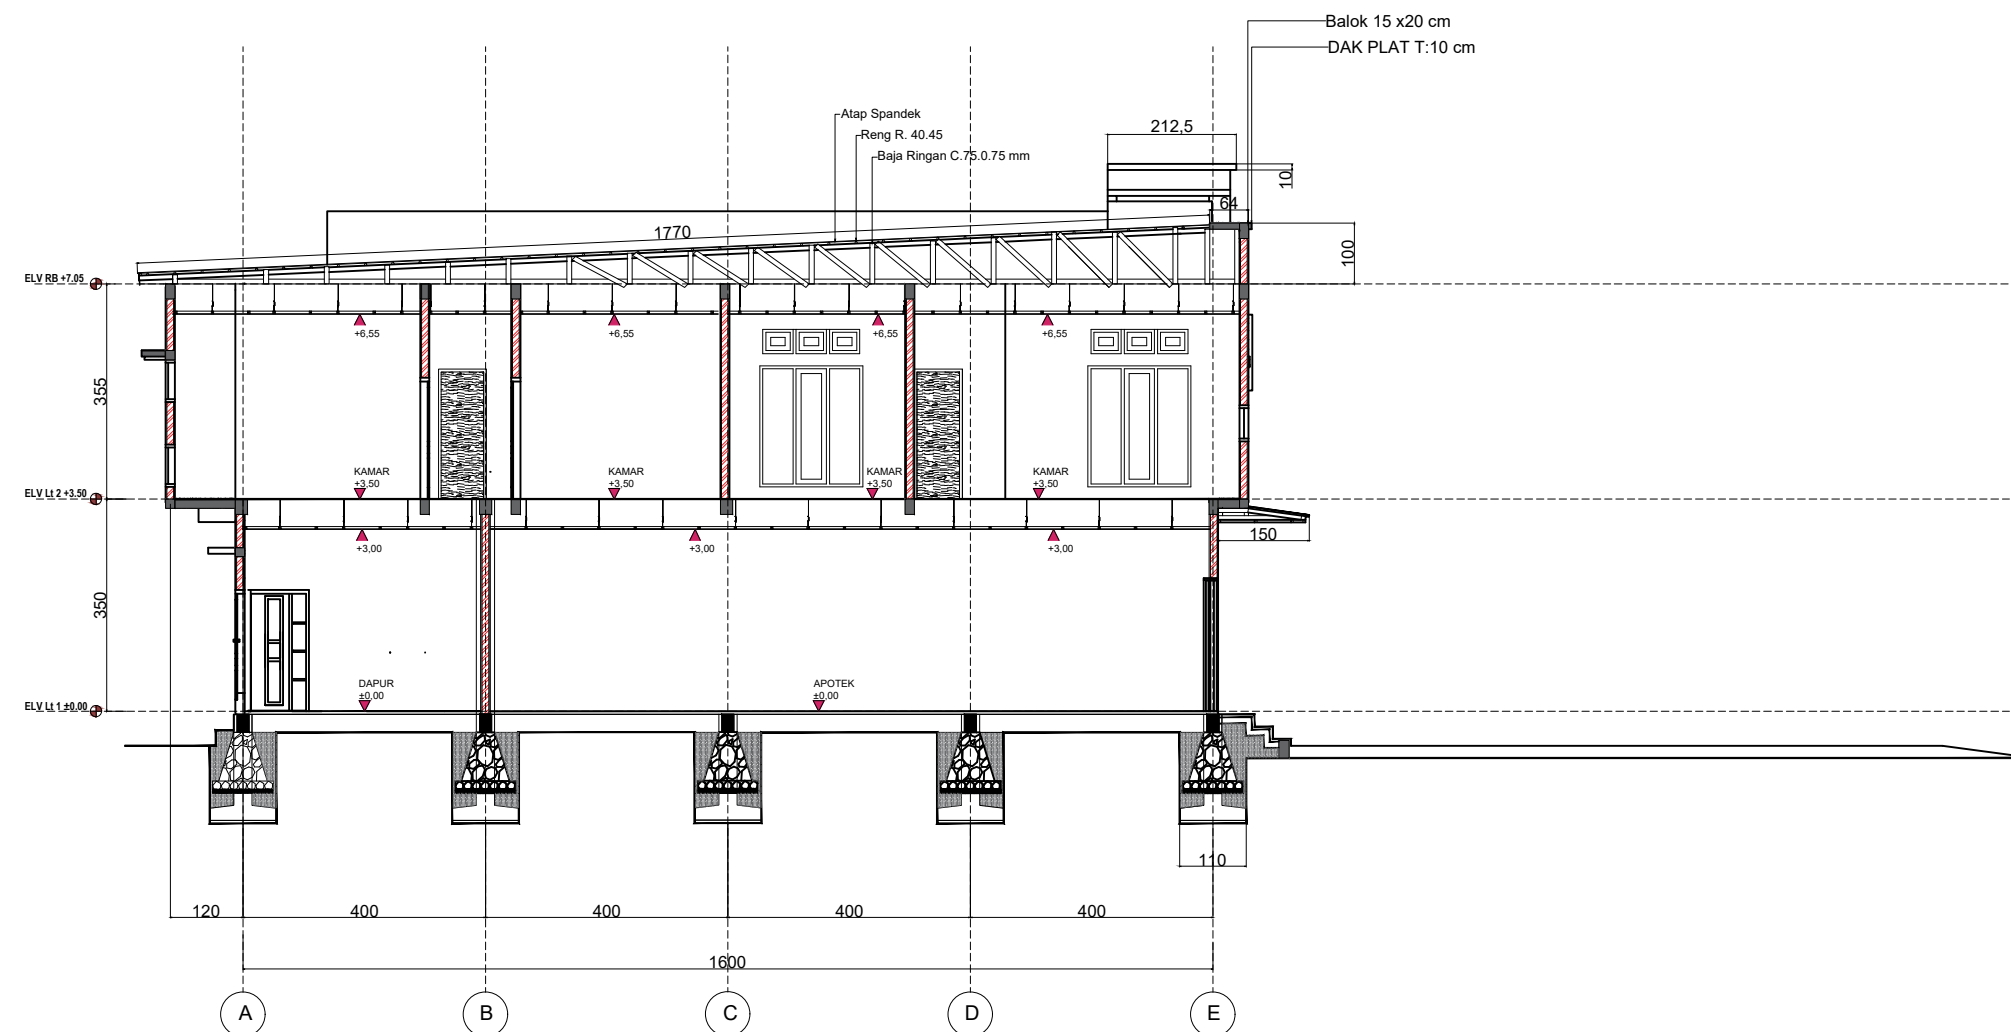

BANGUNAN KOMERSIAL

LOKASI

Kendari, Sulawesi Tenggara

DI GAMBAR OLEH

PARAF

ATIKA, S.Ars

PEMILIK PROYEK

PARAF

AZAM

NAMA GAMBAR

GARIS SEMPADAN JALAN

1.	
2.	
3.	
4.	

SKALA

NO. LEMBAR



LOKASI

Kendari, Sulawesi Tenggara

DI GAMBAR OLEH

PARAF

ATIKA, S.Ars

PEMILIK PROYEK

PARAF

AZAM



NAMA GAMBAR

GARIS SEMPADAN JALAN

1.
2.
3.
4.

SKALA

NO. LEMBAR

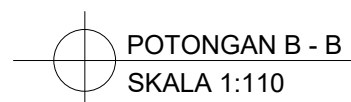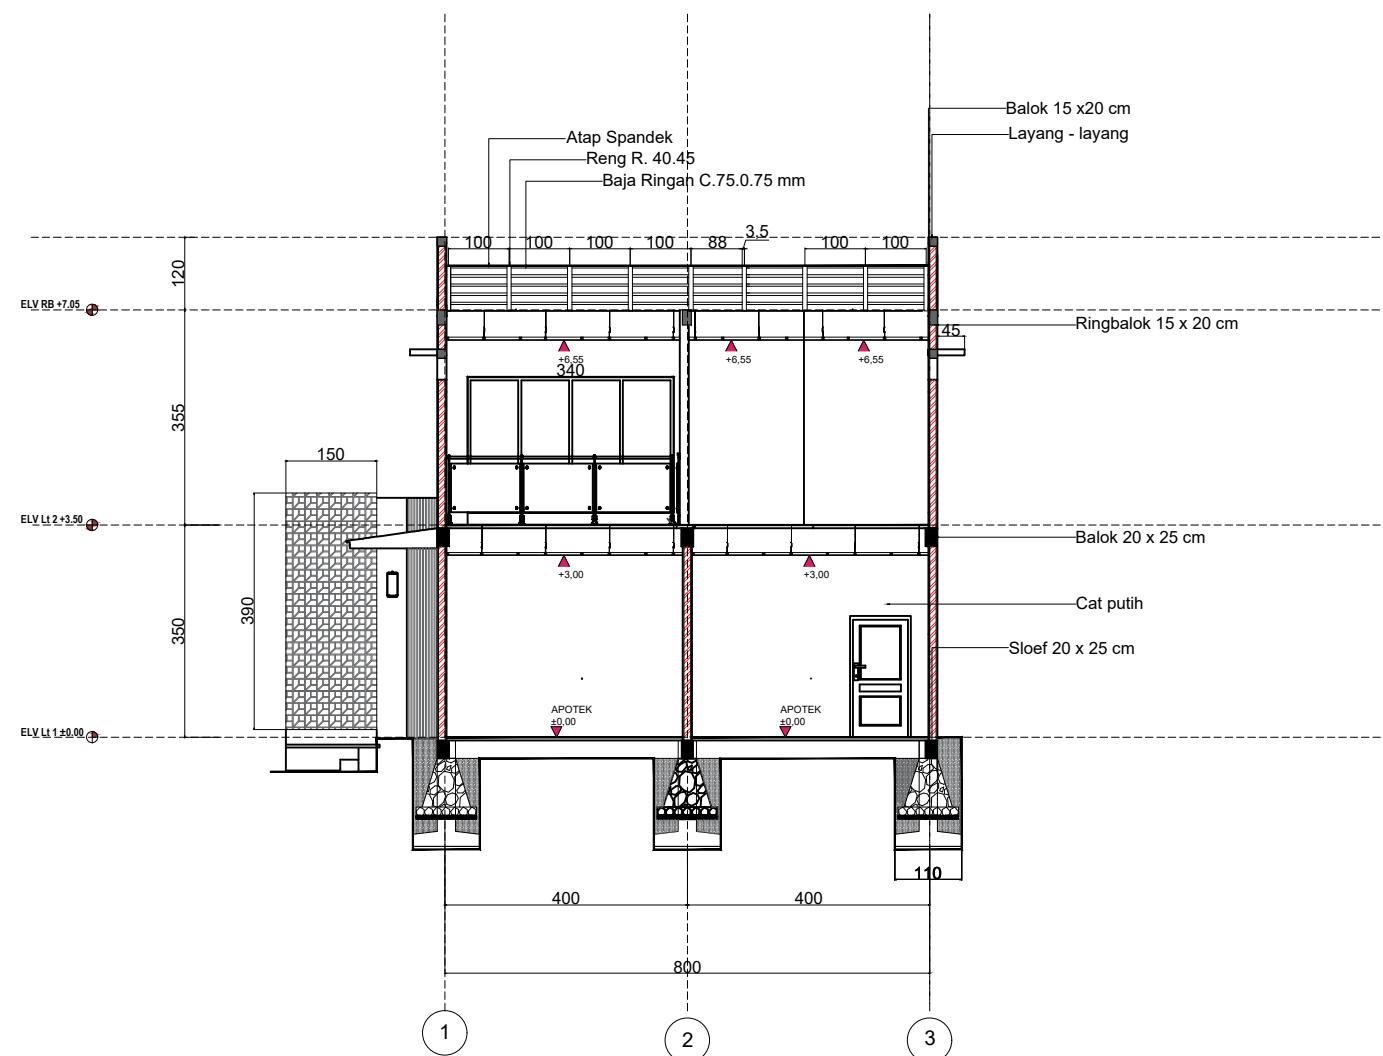



BANGUNAN KOMERSIAL

LOKASI

Kendari, Sulawesi Tenggara

DI GAMBAR OLEH

PARAF

ATIKA, S.Ars

PEMILIK PROYEK

PARAF

AZAM


NAMA GAMBAR

GARIS SEMPADAN JALAN


1.	
2.	
3.	
4.	


SKALA

NO. LEMBAR

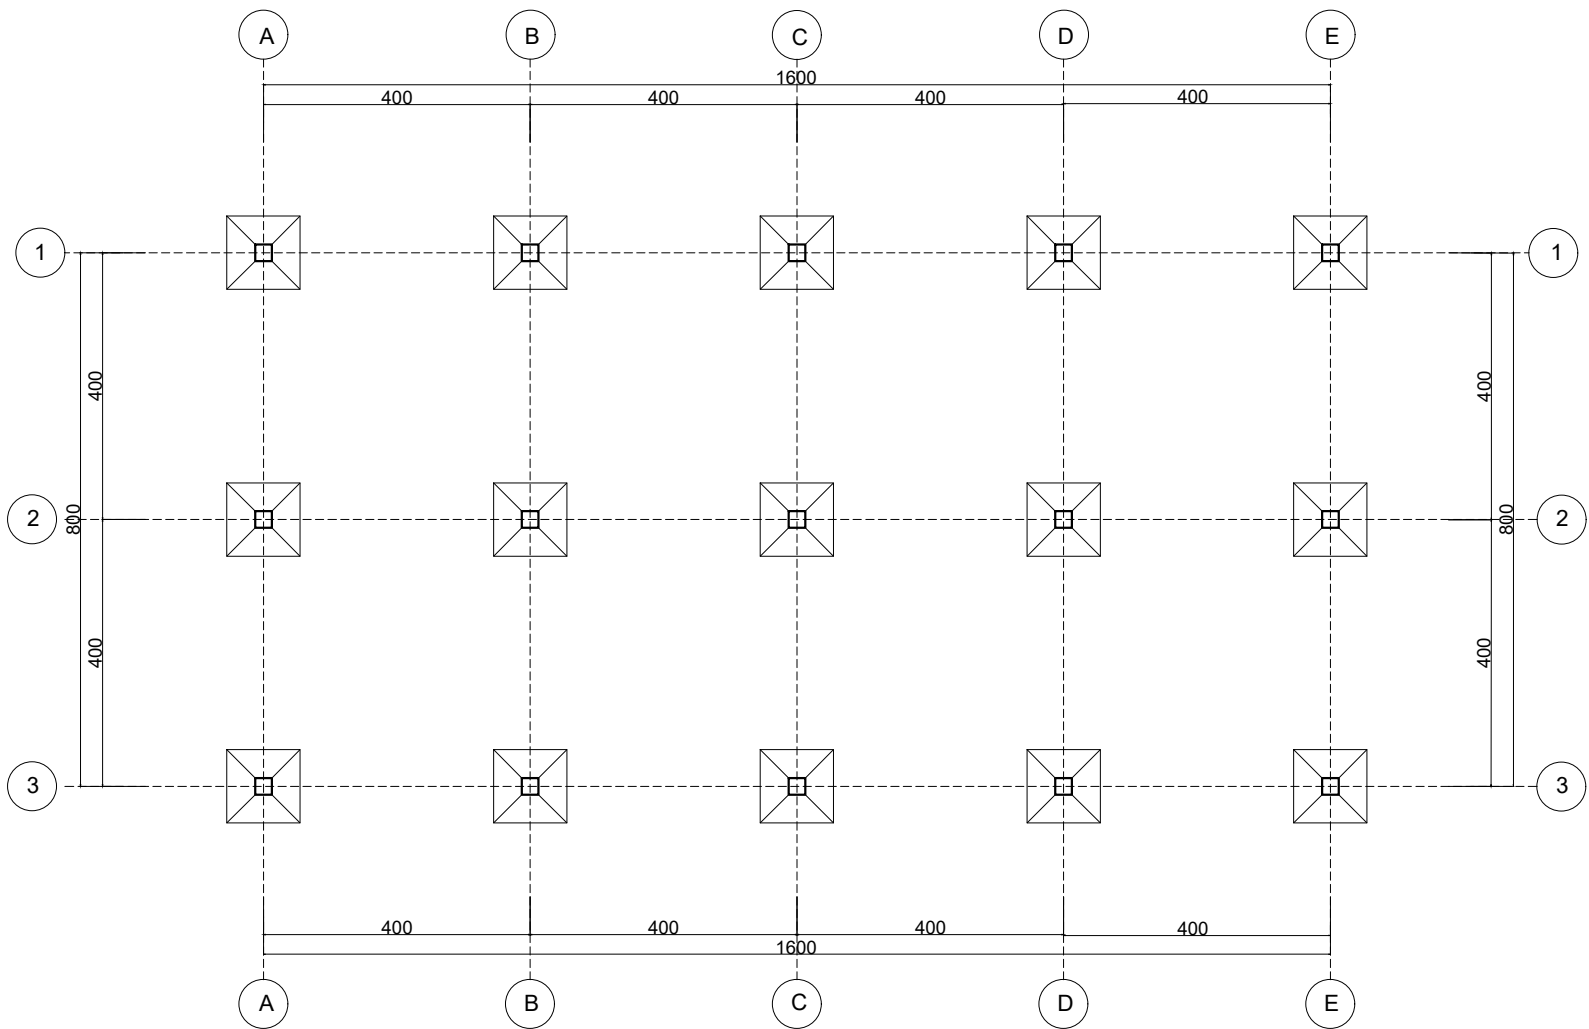

RENCANA PONDASI POER PLAT
SKALA 1:100

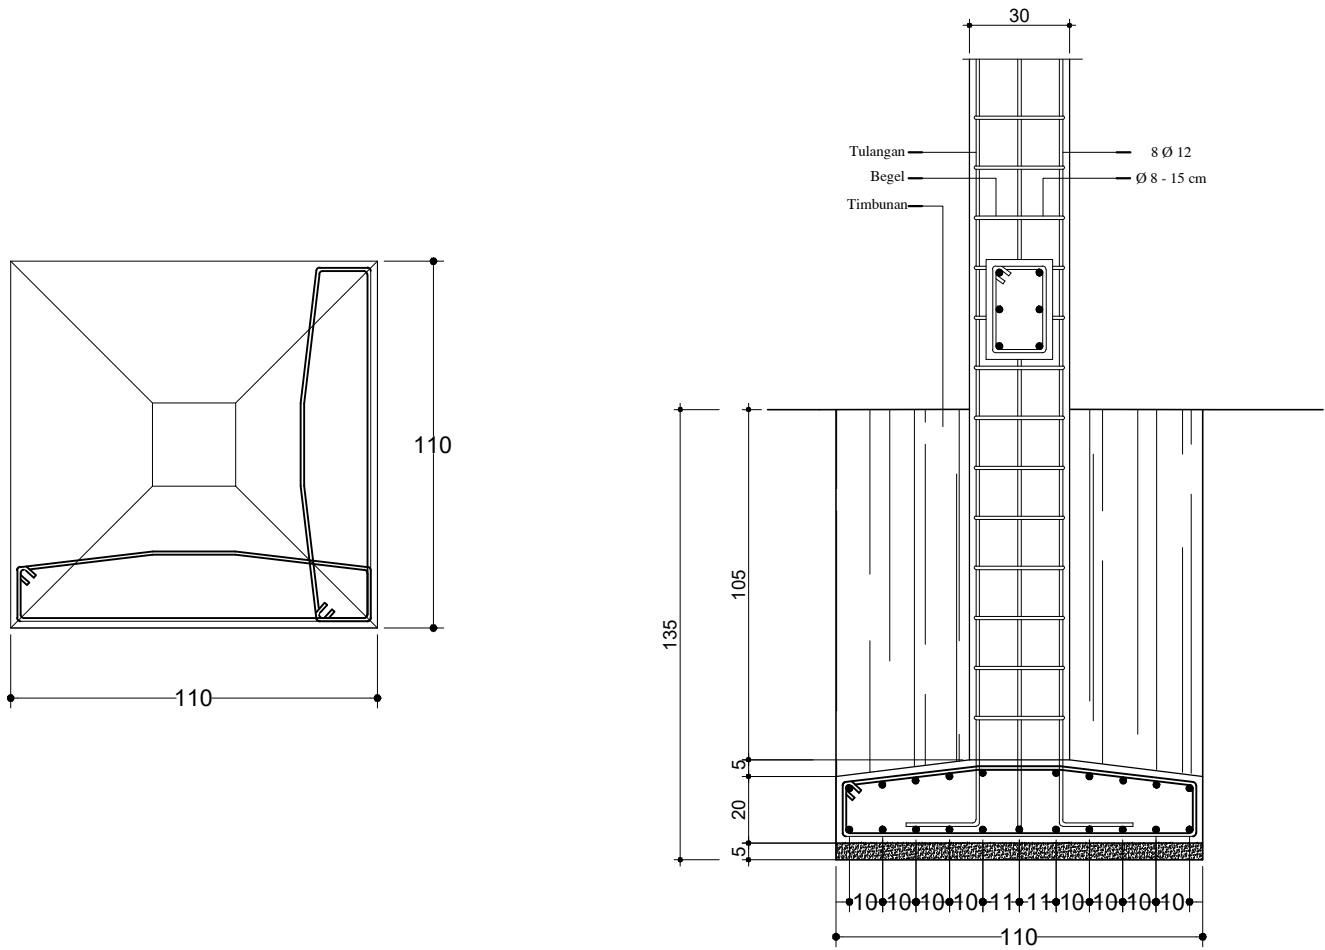

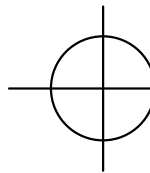 **DETAIL POER PLAT**
SKALA 1:20



BANGUNAN KOMERSIAL

LOKASI

Kendari, Sulawesi Tenggara

DI GAMBAR OLEH

PARAF

ATIKA, S.Ars

PEMILIK PROYEK

PARAF

AZAM


NAMA GAMBAR

GARIS SEMPADAN JALAN

- | | |
|----|--|
| 1. | |
| 2. | |
| 3. | |
| 4. | |

SKALA

NO. LEMBAR

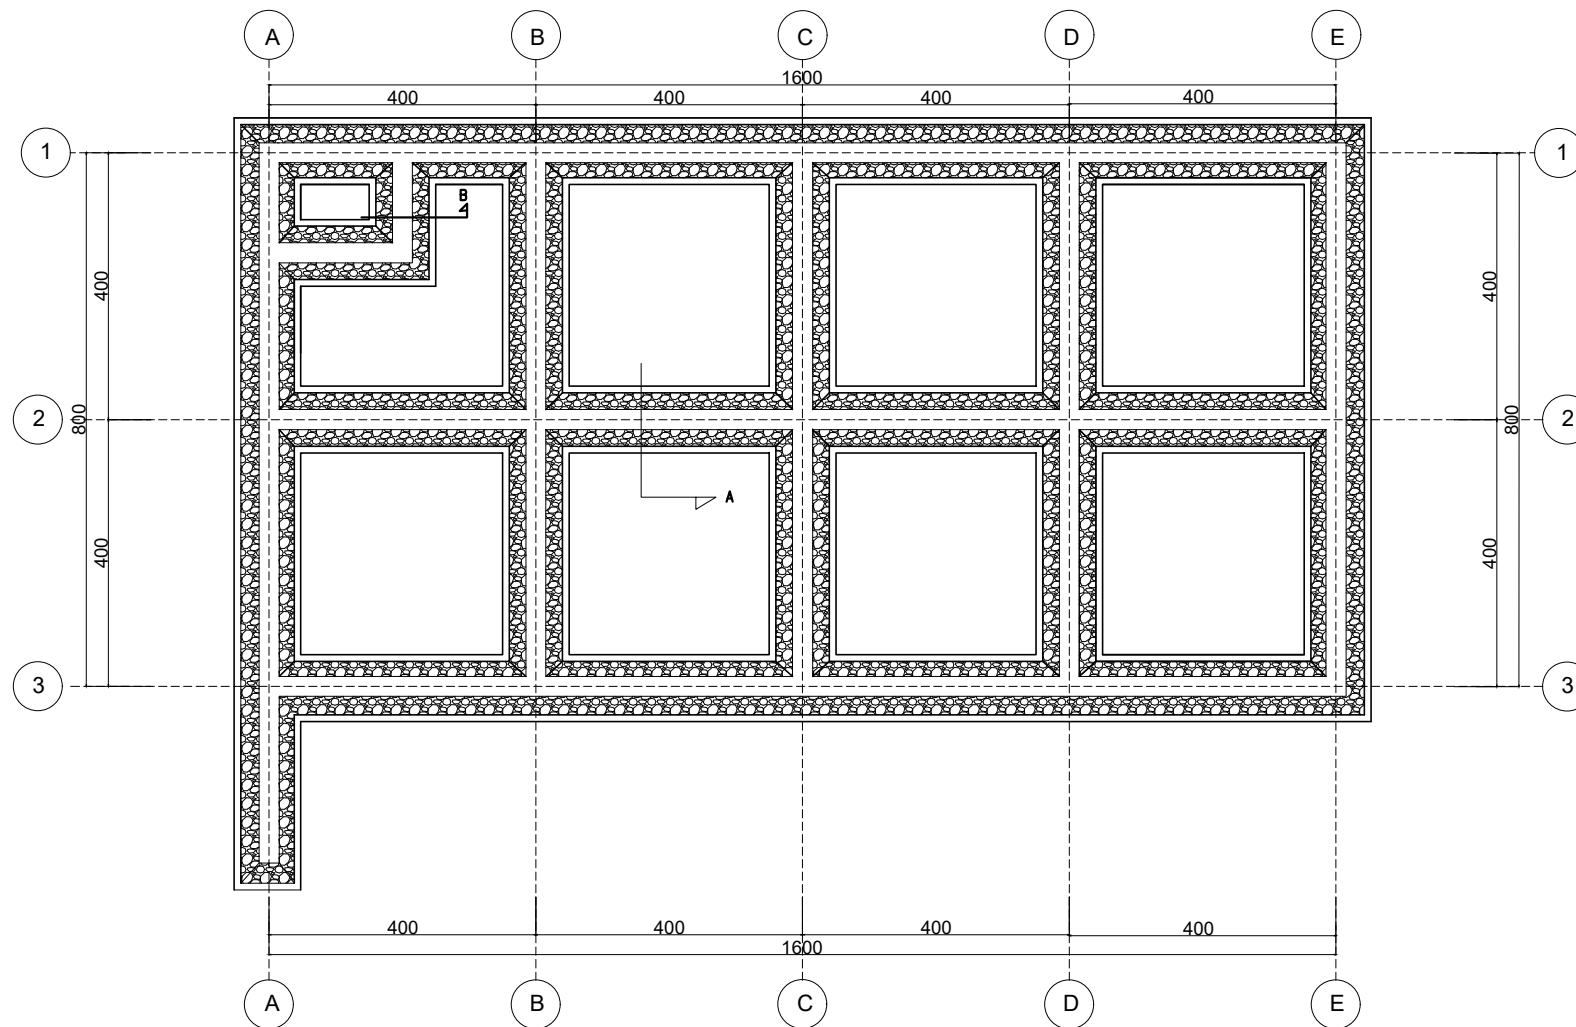

RENCANA PONDASI MENERUS
SKALA 1:100



BANGUNAN KOMERSIAL

LOKASI

Kendari, Sulawesi Tenggara

DI GAMBAR OLEH

PARAF

ATIKA, S.Ars

PEMILIK PROYEK

PARAF

AZAM


NAMA GAMBAR

GARIS SEMPADAN JALAN


1.	
2.	
3.	
4.	

SKALA

NO. LEMBAR

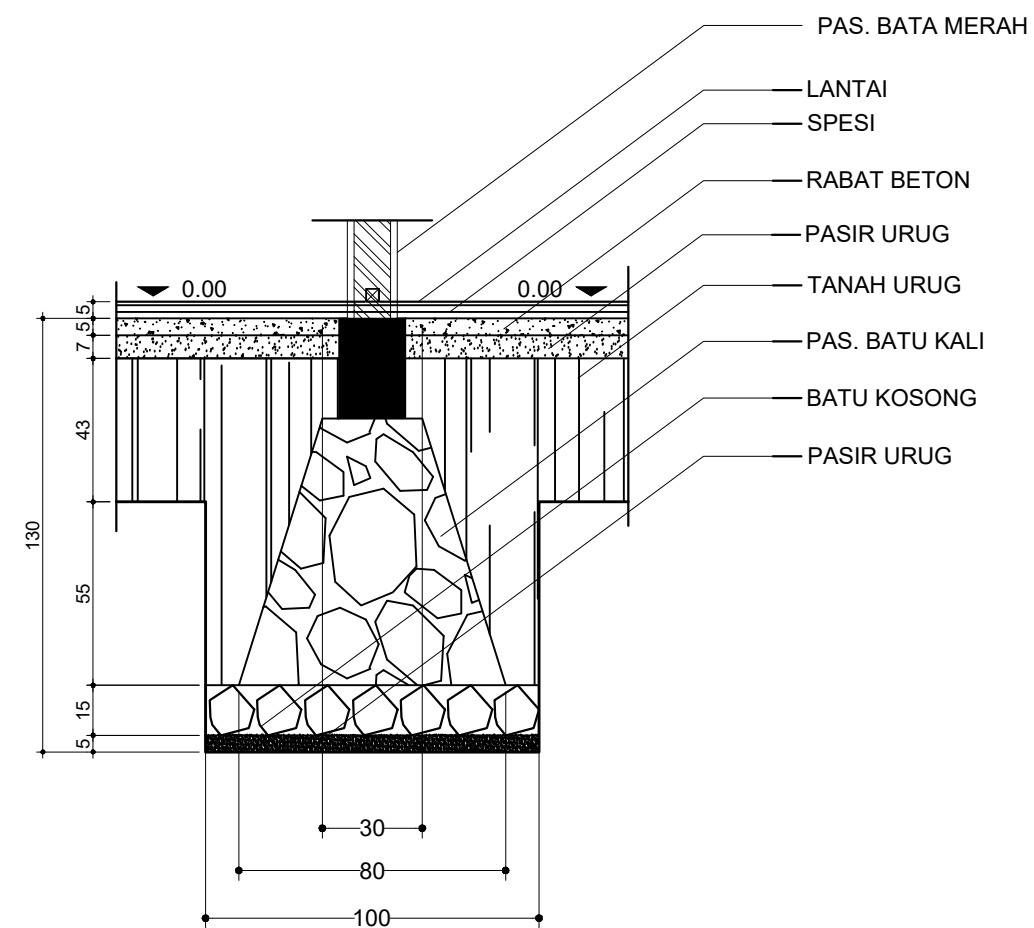

DETAIL PONDASI A
SKALA 1 :20

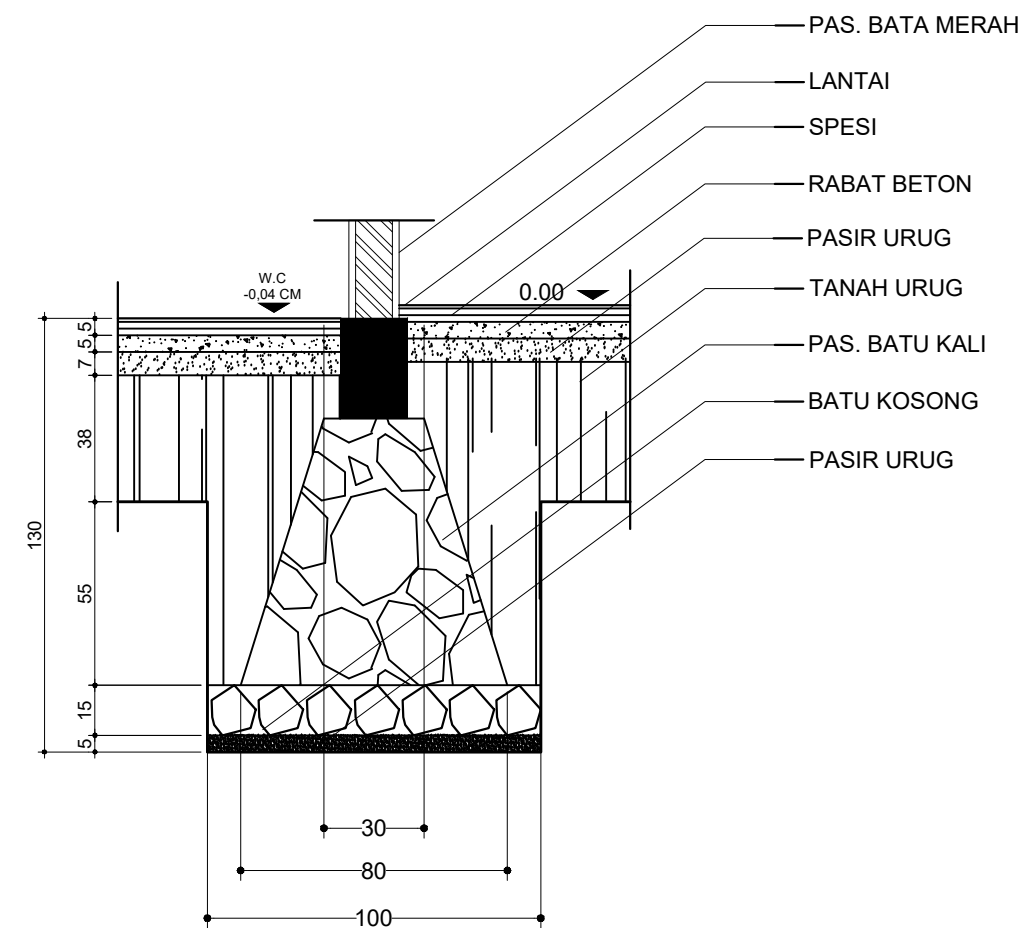

 **DETAIL PONDASI B**
SKALA 1 : 20



BANGUNAN KOMERSIAL

LOKASI

Kendari, Sulawesi Tenggara

DI GAMBAR OLEH

PARAF

ATIKA, S.Ars

PEMILIK PROYEK

PARAF

AZAM

NAMA GAMBAR

GARIS SEMPADAN JALAN

1.
2.
3.
4.

SKALA

NO. LEMBAR



BANGUNAN KOMERSIAL

LOKASI

Kendari, Sulawesi Tenggara

DI GAMBAR OLEH

PARAF

ATIKA, S.Ars

PEMILIK PROYEK

PARAF

AZAM

NAMA GAMBAR

GARIS SEMPADAN JALAN

1.


2.

3.

4.

SKALA

NO. LEMBAR

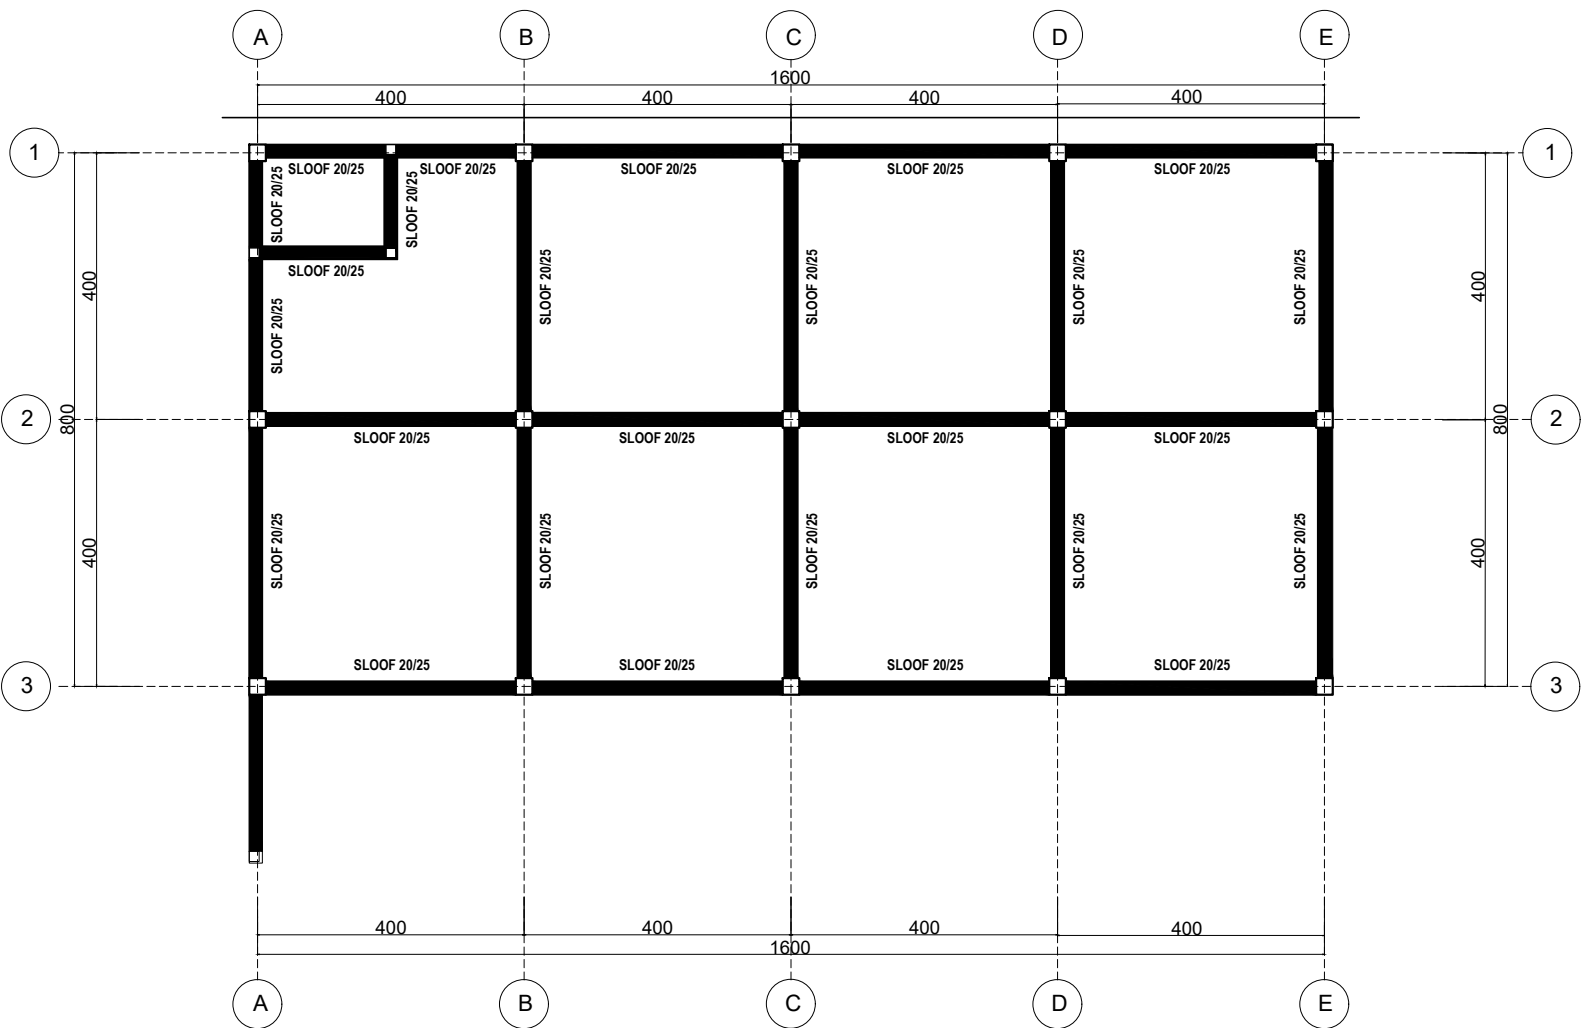

RENCANA SLOEF
SKALA 1:100



BANGUNAN KOMERSIAL

LOKASI

Kendari, Sulawesi Tenggara

DI GAMBAR OLEH

PARAF

ATIKA, S.Ars

PEMILIK PROYEK

PARAF

AZAM


NAMA GAMBAR

GARIS SEMPADAN JALAN

1.	
2.	
3.	
4.	

SKALA

NO. LEMBAR

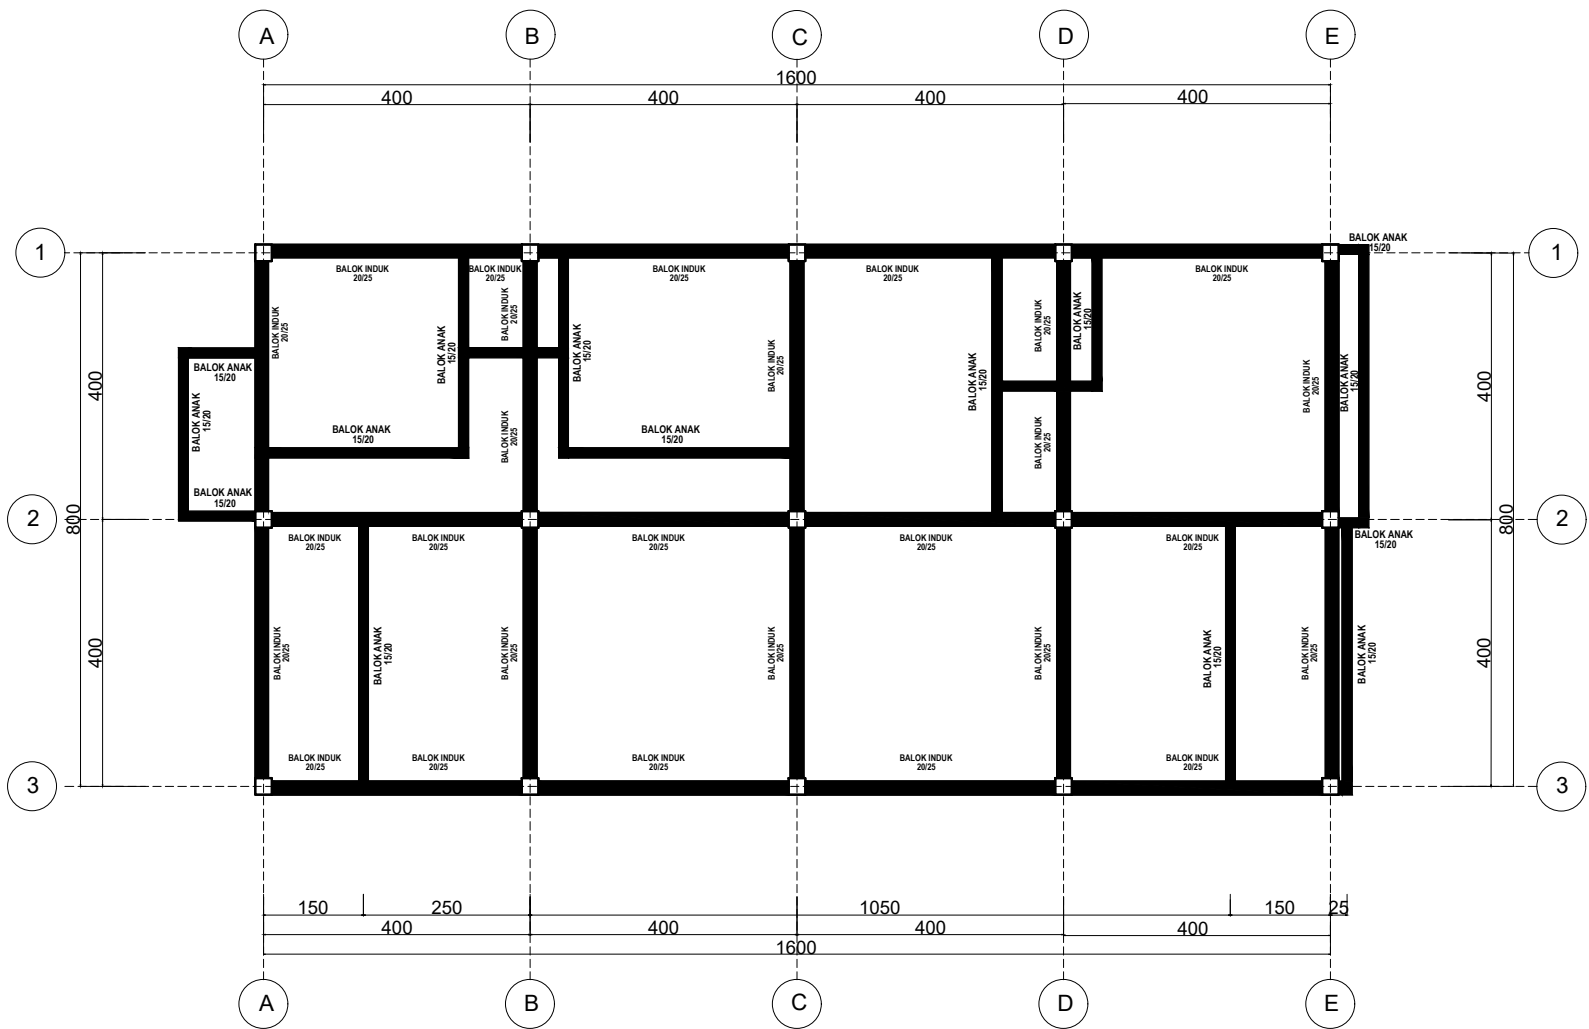

BALOK INDUK (BI), BALOK ANAK (BA)
SKALA 1:100



BANGUNAN KOMERSIAL

LOKASI

Kendari, Sulawesi Tenggara

DI GAMBAR OLEH

PARAF

ATIKA, S.Ars

PEMILIK PROYEK

PARAF

AZAM

NAMA GAMBAR

GARIS SEMPADAN JALAN


1.	
2.	
3.	
4.	

SKALA

NO. LEMBAR



RENCANA RINGBALK
SKALA 1:100

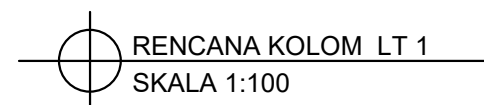



BANGUNAN KOMERSIAL

LOKASI

Kendari, Sulawesi Tenggara

DI GAMBAR OLEH

PARAF

ATIKA, S.Ars

PEMILIK PROYEK

PARAF

AZAM


NAMA GAMBAR

GARIS SEMPADAN JALAN

1.	
2.	
3.	
4.	

SKALA

NO. LEMBAR

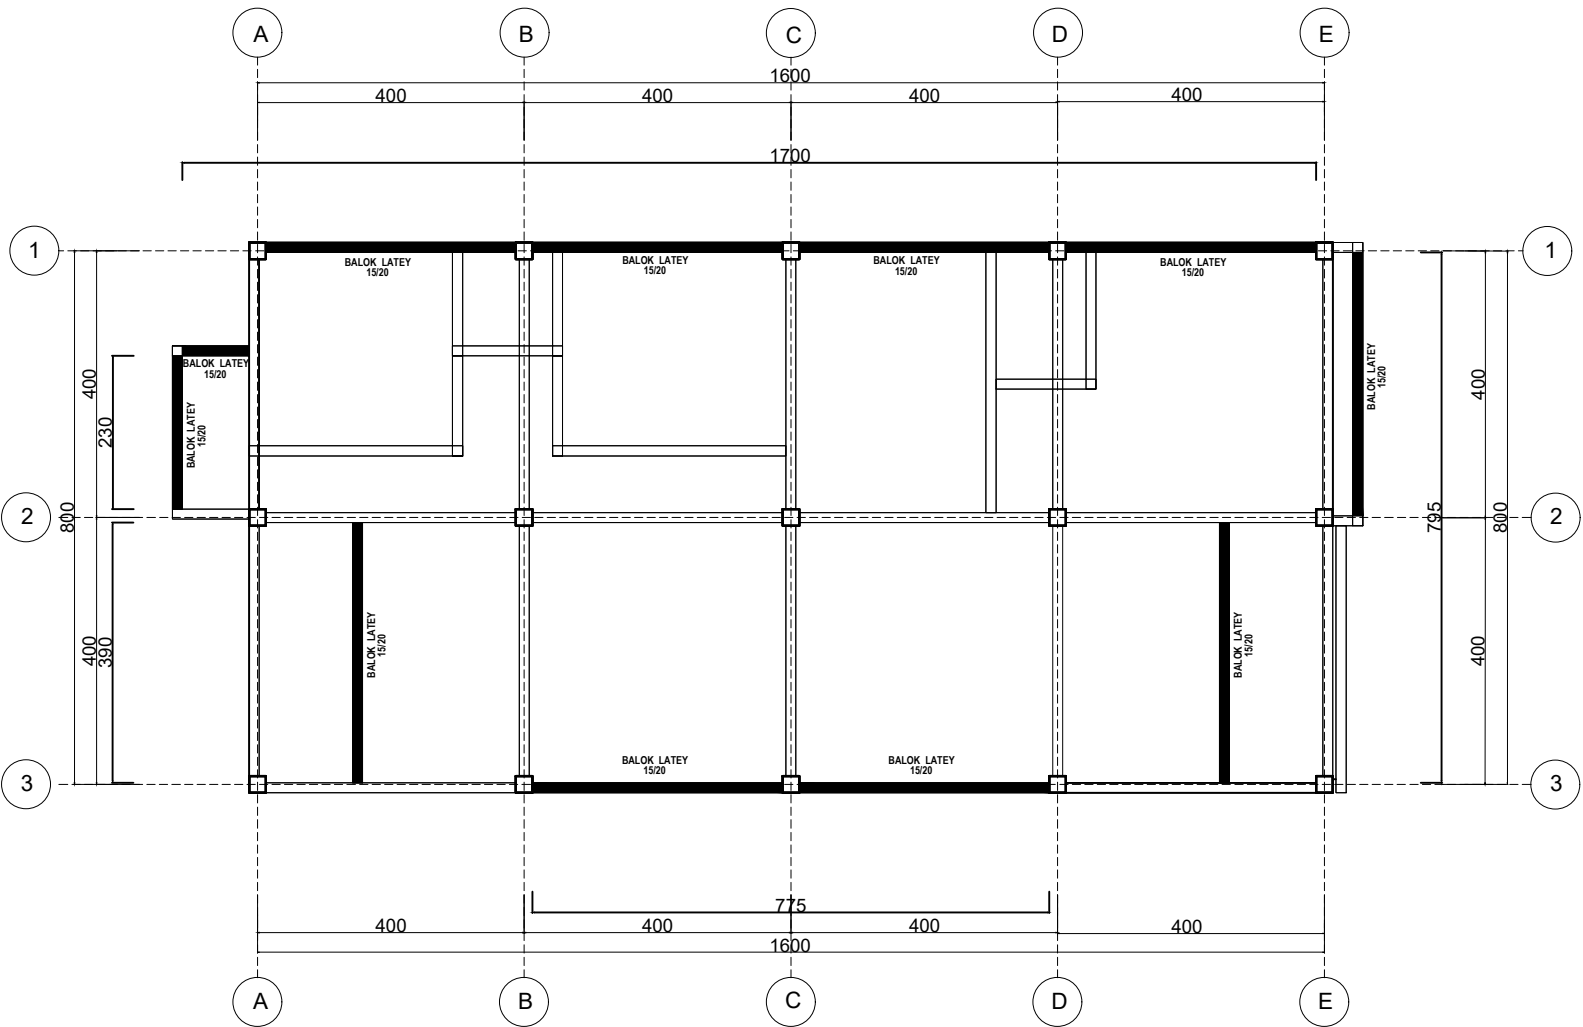

RENCANA BALOK LATEY
SKALA 1:100



BANGUNAN KOMERSIAL

LOKASI

Kendari, Sulawesi Tenggara

DI GAMBAR OLEH

PARAF

ATIKA, S.Ars

PEMILIK PROYEK

PARAF

AZAM


NAMA GAMBAR

GARIS SEMPADAN JALAN



1.	
2.	
3.	
4.	

SKALA


NO. LEMBAR

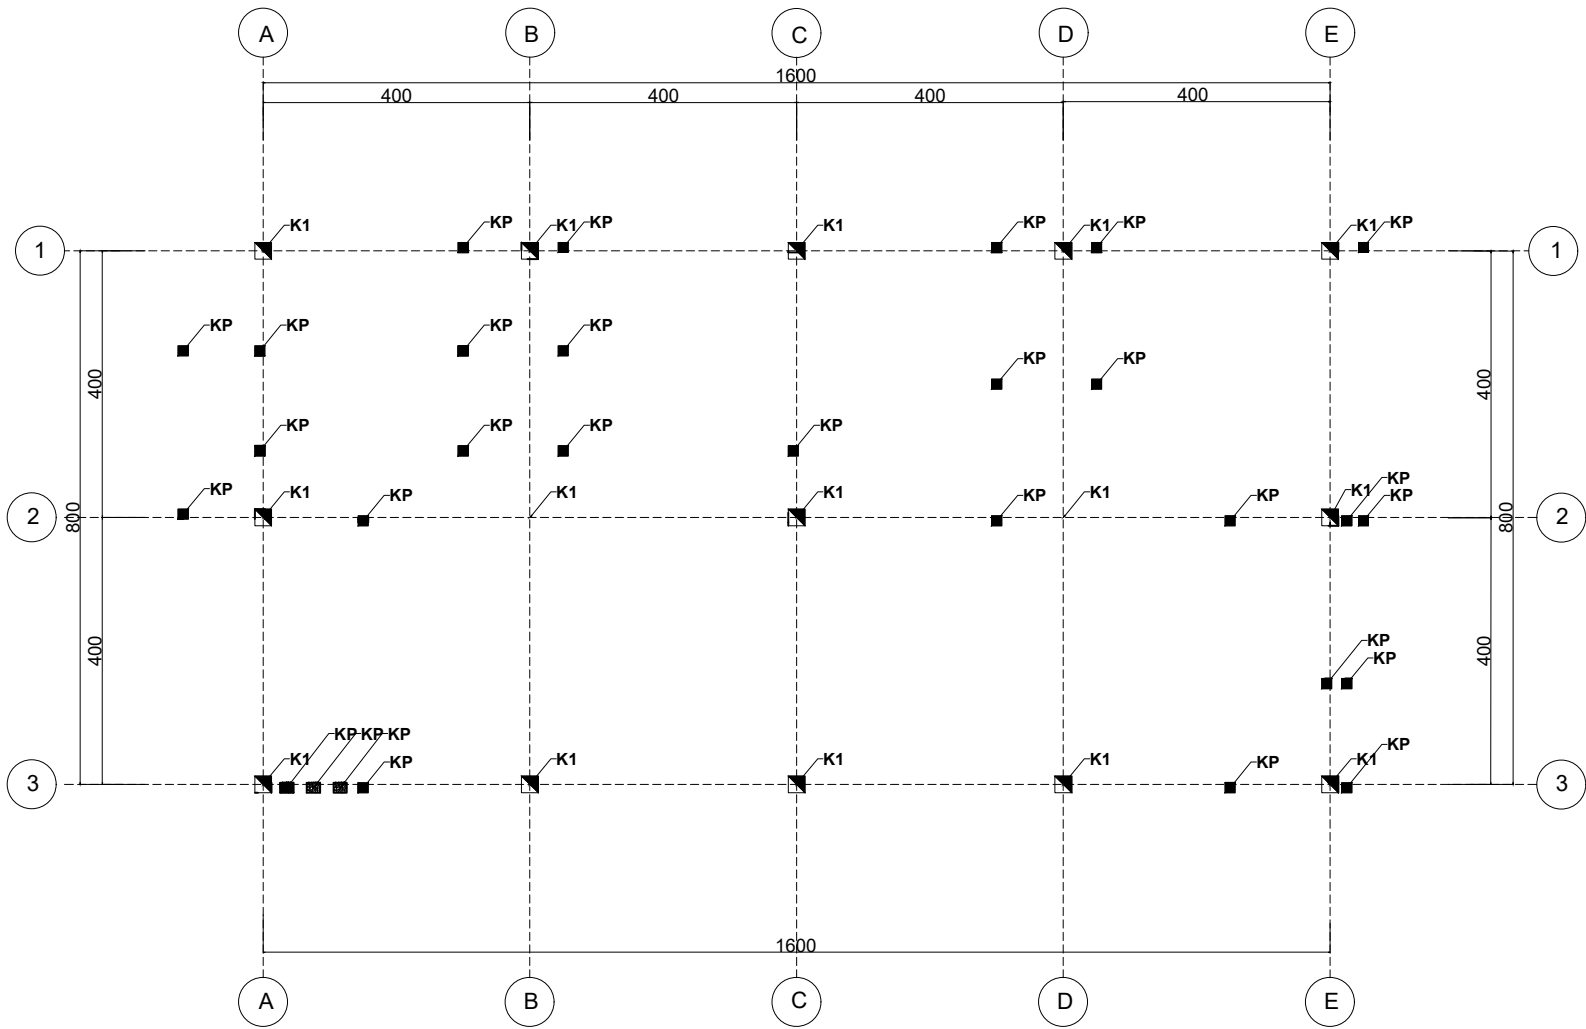





RENCANA KOLOM LT 2
SKALA 1:100

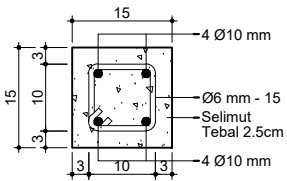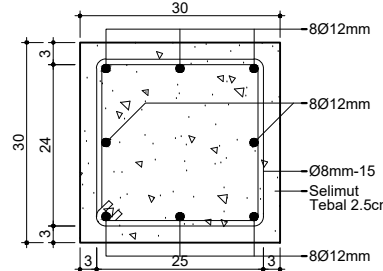NOTASI	DETAIL KP (KOLOM PRAKTIS)	NOTASI	DETAIL K1 (KOLOM 1)
GAMBAR KOLOM (KP)		GAMBAR KOLOM (K1)	
	Dimensi		Dimensi
	Tulangan Atas		Tulangan Atas
	Tulangan Tengah		Tulangan Tengah
	Tulangan Bawah		Tulangan Bawah
	Beugel / Sengkang		Beugel / Sengkang

TABEL STRUKTUR KOLOM
SKALA 1:10

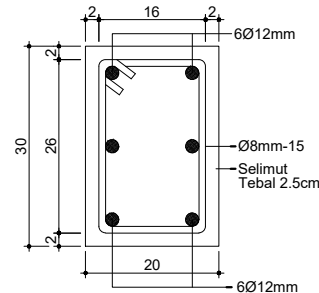NOTASI	DETAIL SL (SLOOF)
GAMBAR SLOOF (SL)	
	Dimensi
	Tulangan Atas
	Tulangan Bawah
	Beugel / Sengkang

TABEL STRUKTUR SLOOF
SKALA 1:10

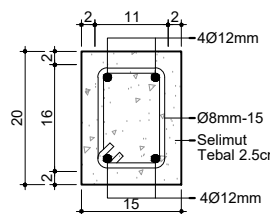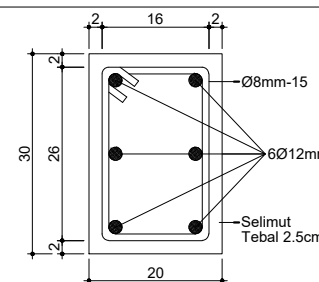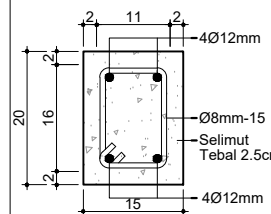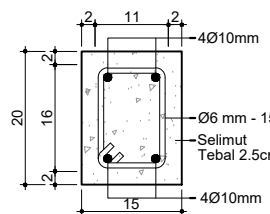NOTASI	DETAIL BA (BALOK ANAK)	NOTASI	DETAIL BI (BALOK INDUK)	NOTASI	DETAIL BL (BALOK LATEY)	NOTASI	DETAIL RB (RINGBALK)
GAMBAR BALOK ANAK (BA)		GAMBAR BALOK INDUK (BI)		GAMBAR B.LATEY (BL)		GAMBAR RINGBALK (RB)	
	Dimensi		Dimensi		Dimensi		Dimensi
	Tulangan Atas		Tulangan Atas		Tulangan Atas		Tulangan Atas
	Tulangan Bawah		Tulangan Bawah		Tulangan Bawah		Tulangan Bawah
	Tulangan Tengah		Tulangan Tengah		Tulangan Tengah		Tulangan Tengah
	Beugel / Sengkang		Beugel / Sengkang		Beugel / Sengkang		Beugel / Sengkang

TABEL STRUKTUR B.INDUK+B.ANAK
SKALA 1:10

TABEL STRUKTUR B.LATEY+RINGBALK
SKALA 1:10



BANGUNAN KOMERSIAL

LOKASI

Kendari, Sulawesi Tenggara

DI GAMBAR OLEH

PARAF

ATIKA, S.Ars

PEMILIK PROYEK

PARAF

AZAM

NAMA GAMBAR

GARIS SEMPADAN JALAN

- 1.
- 2.
- 3.
- 4.

SKALA

NO. LEMBAR



BANGUNAN KOMERSIAL

LOKASI

Kendari, Sulawesi Tenggara

DI GAMBAR OLEH

PARAF

ATIKA, S.Ars

PEMILIK PROYEK

PARAF

AZAM


NAMA GAMBAR

GARIS SEMPADAN JALAN

1.	
2.	
3.	
4.	

SKALA

NO. LEMBAR

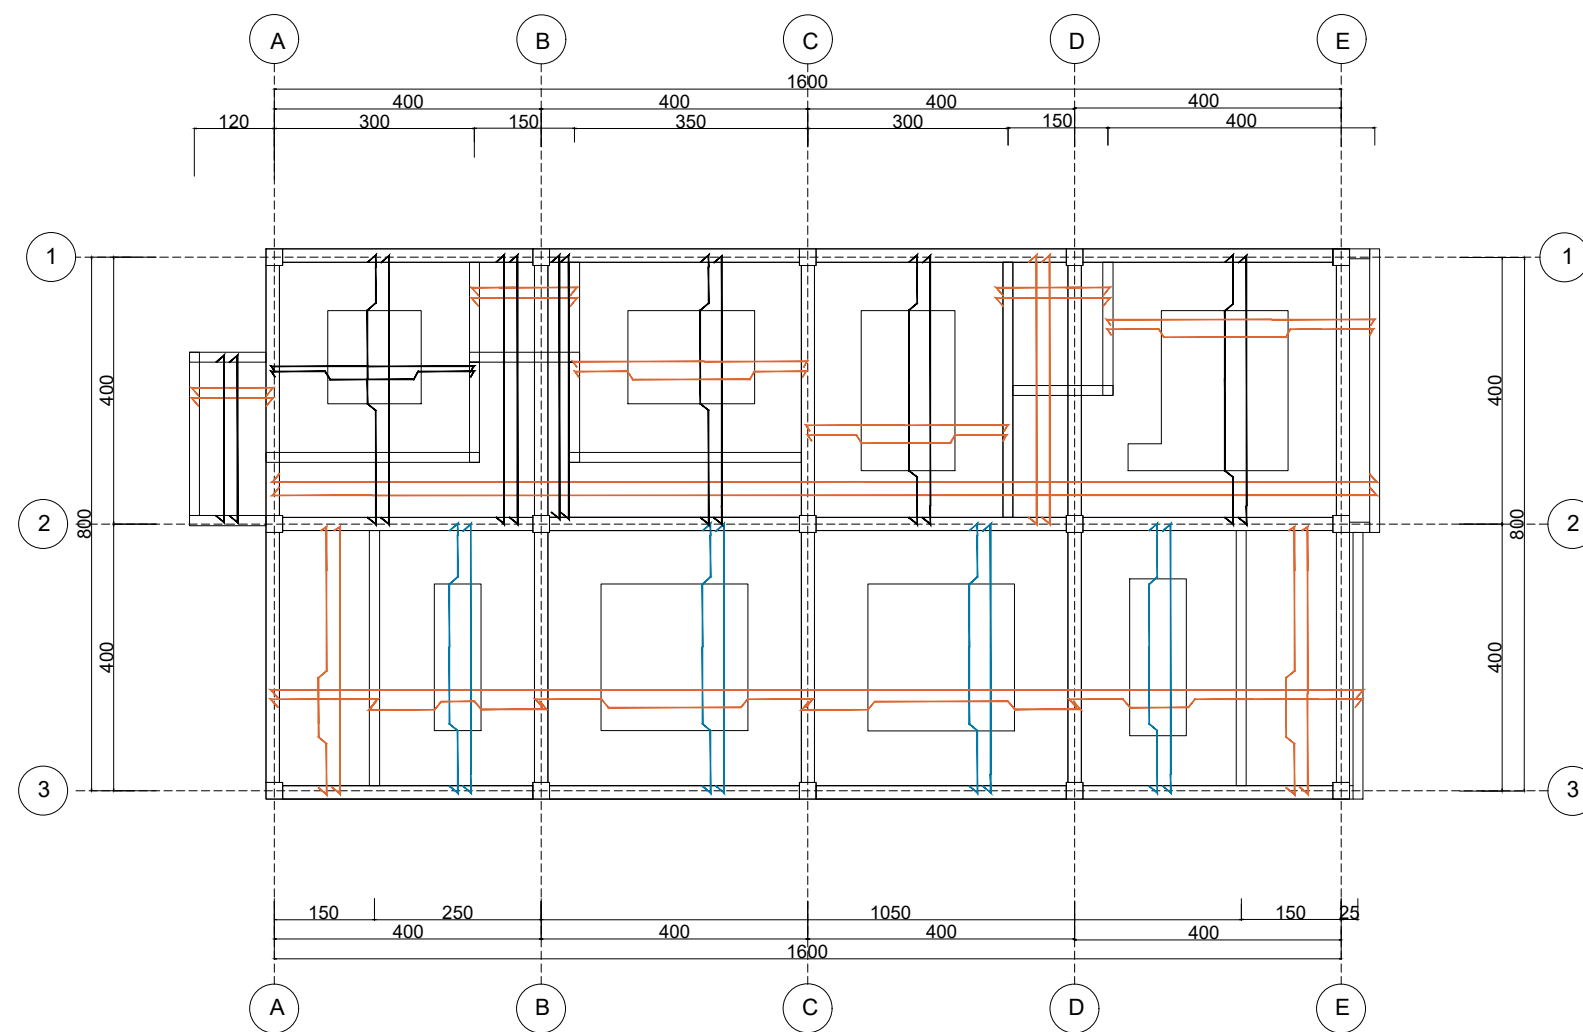

RENCANA PLAT LANTAI
SKALA 1:100



BANGUNAN KOMERSIAL

LOKASI

Kendari, Sulawesi Tenggara

DI GAMBAR OLEH

PARAF

ATIKA, S.Ars

PEMILIK PROYEK

PARAF

AZAM


NAMA GAMBAR

GARIS SEMPADAN JALAN

1.	
2.	
3.	
4.	

SKALA


NO. LEMBAR

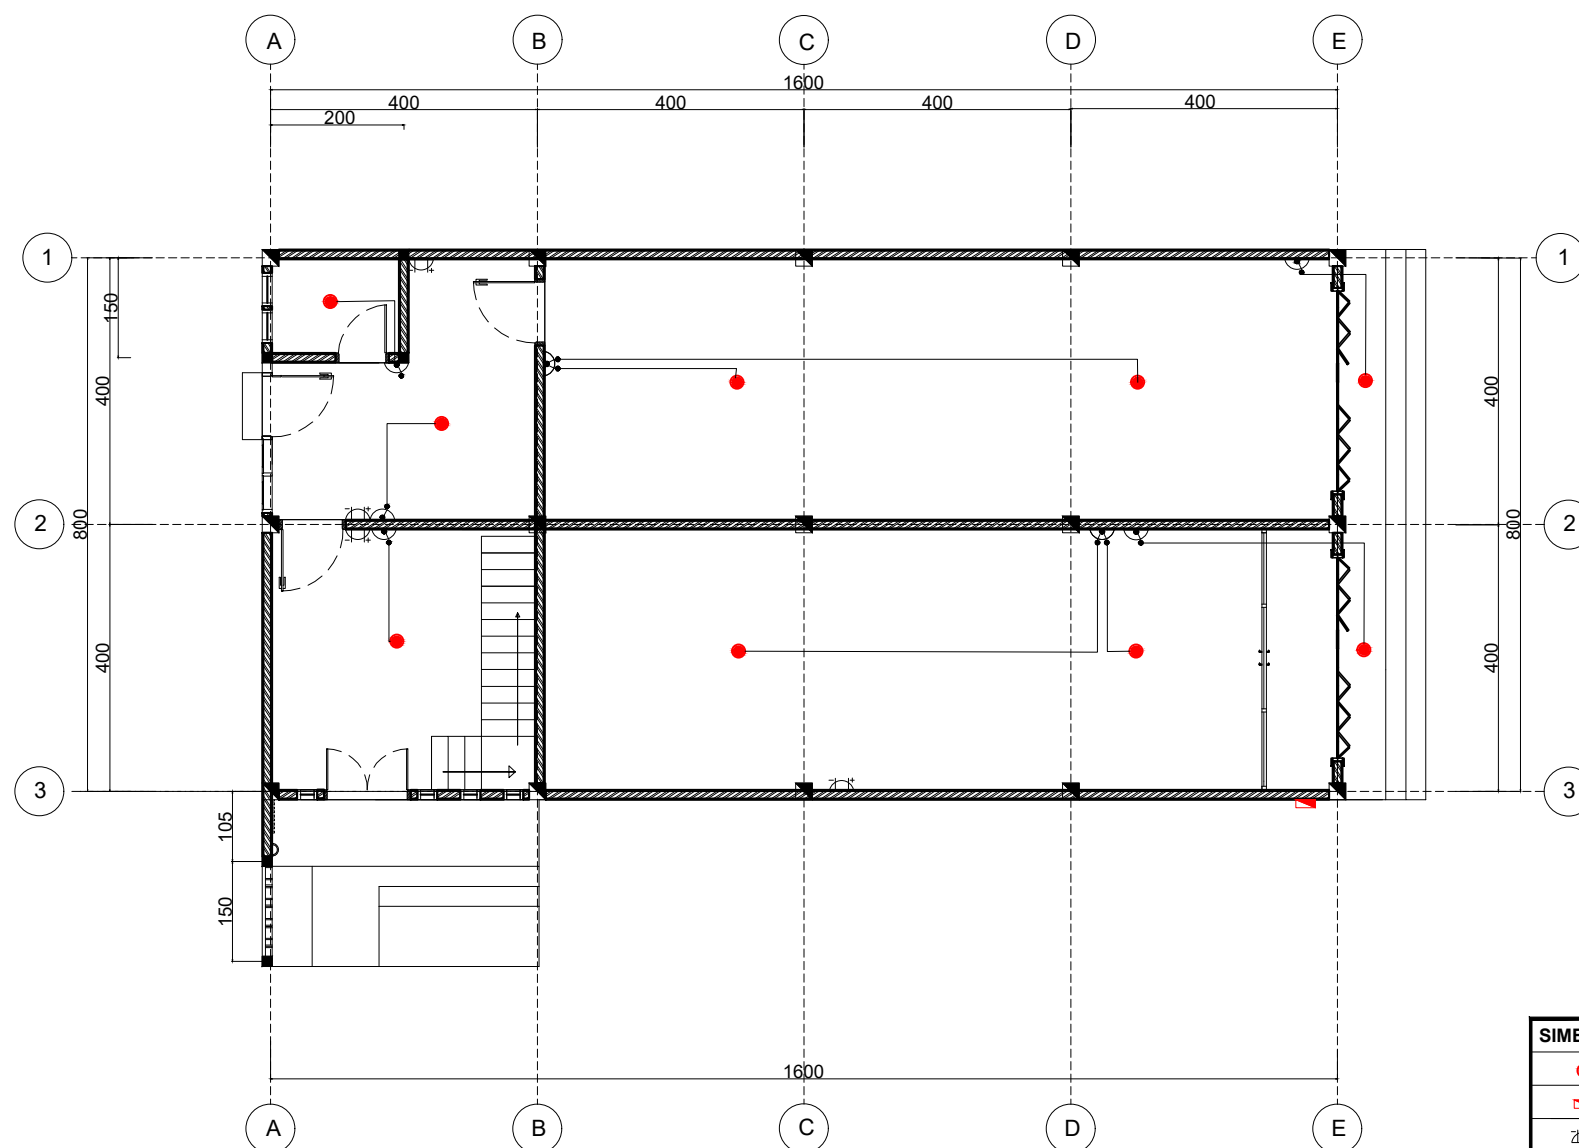

TABEL KEBUTUHAN BAHAN LISTRIK

SIMBOL	KETERANGAN	JUMLAH
●	Lampu	9 Buah
⏻	Box MCB 450 Kwh	1 Buah
⏻	Stop Kontak	4 Buah
⏻	Sakelar Tunggal	5 Buah
⏻	Sakelar Ganda	2 Buah

RENCANA INSTALASI LISTRIK LT 1
SKALA 1:100

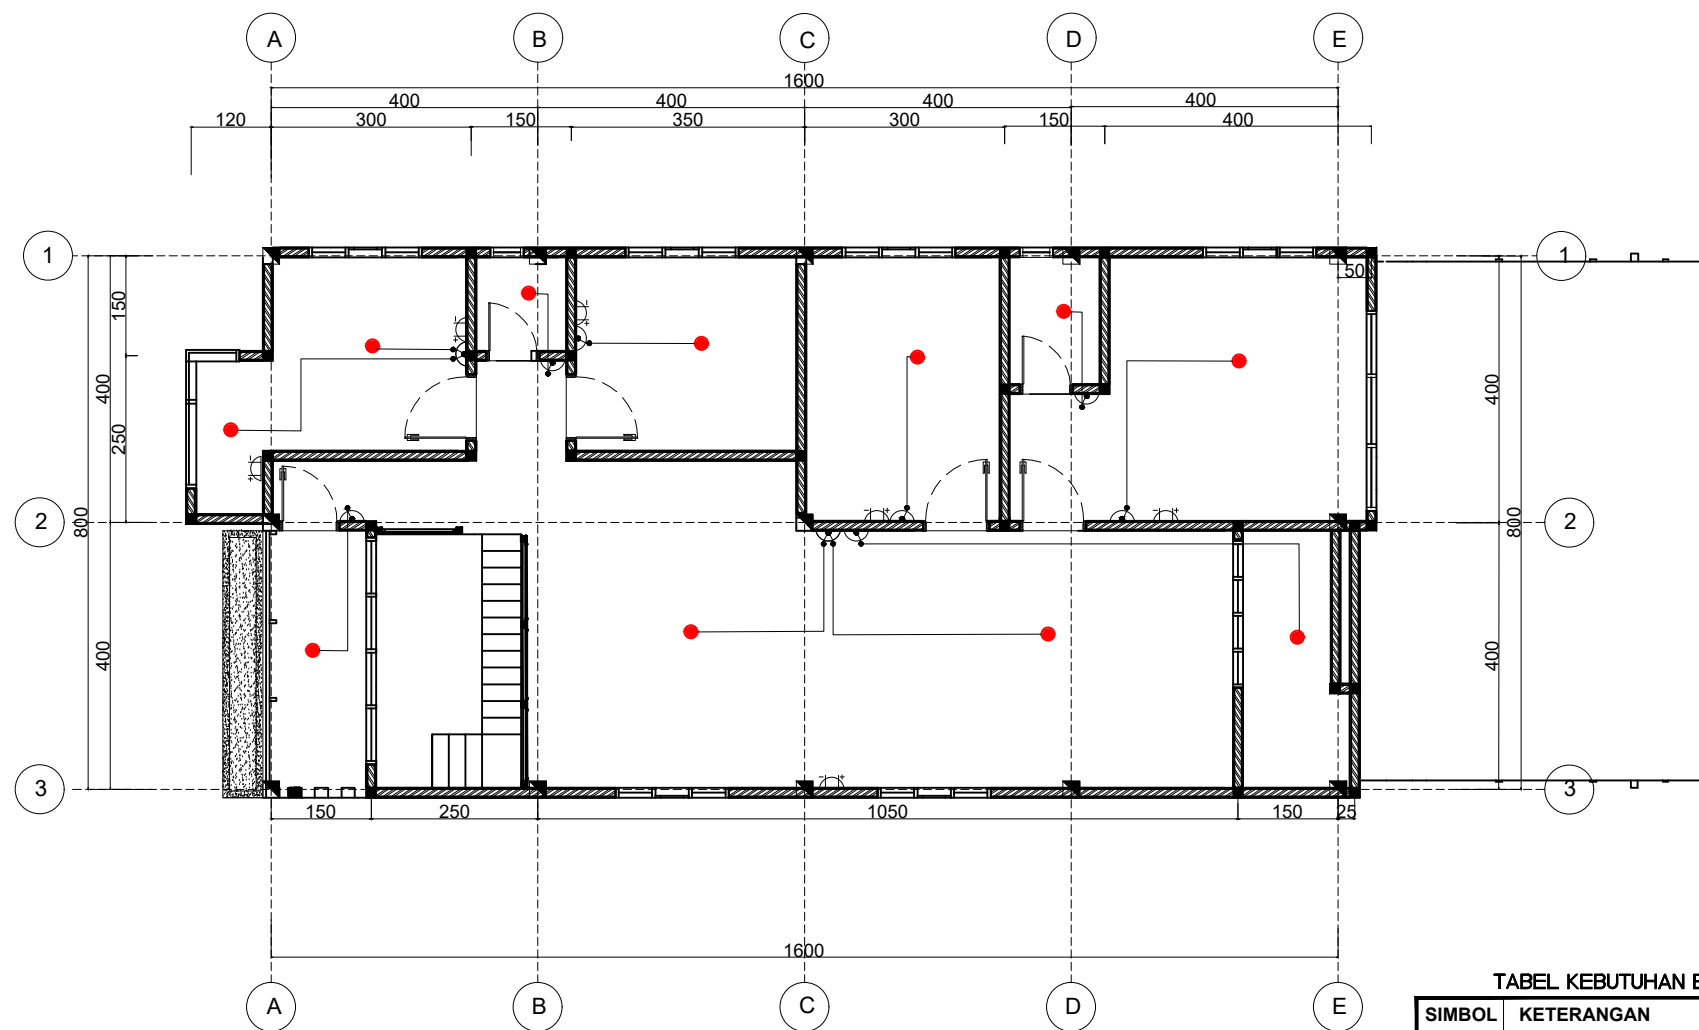

TABEL KEBUTUHAN BAHAN LISTRIK		
SIMBOL	KETERANGAN	JUMLAH
●	Lampu	12 Buah
⏏	Stop Kontak	6 Buah
⏏	Sakelar Tunggal	7 Buah
⏏	Sakelar Ganda	2 Buah

RENCANA INSTALASI LISTRIK LT 2
SKALA 1:100



BANGUNAN KOMERSIAL

LOKASI

Kendari, Sulawesi Tenggara

DI GAMBAR OLEH

PARAF

ATIKA, S.Ars

PEMILIK PROYEK

PARAF

AZAM

NAMA GAMBAR

GARIS SEMPADAN JALAN

1.	
2.	
3.	
4.	

SKALA

NO. LEMBAR



BANGUNAN KOMERSIAL

LOKASI

Kendari, Sulawesi Tenggara

DI GAMBAR OLEH

PARAF

ATIKA, S.Ars

PEMILIK PROYEK

PARAF

AZAM

NAMA GAMBAR

GARIS SEMPADAN JALAN

1.


2.

3.

4.

SKALA

NO. LEMBAR

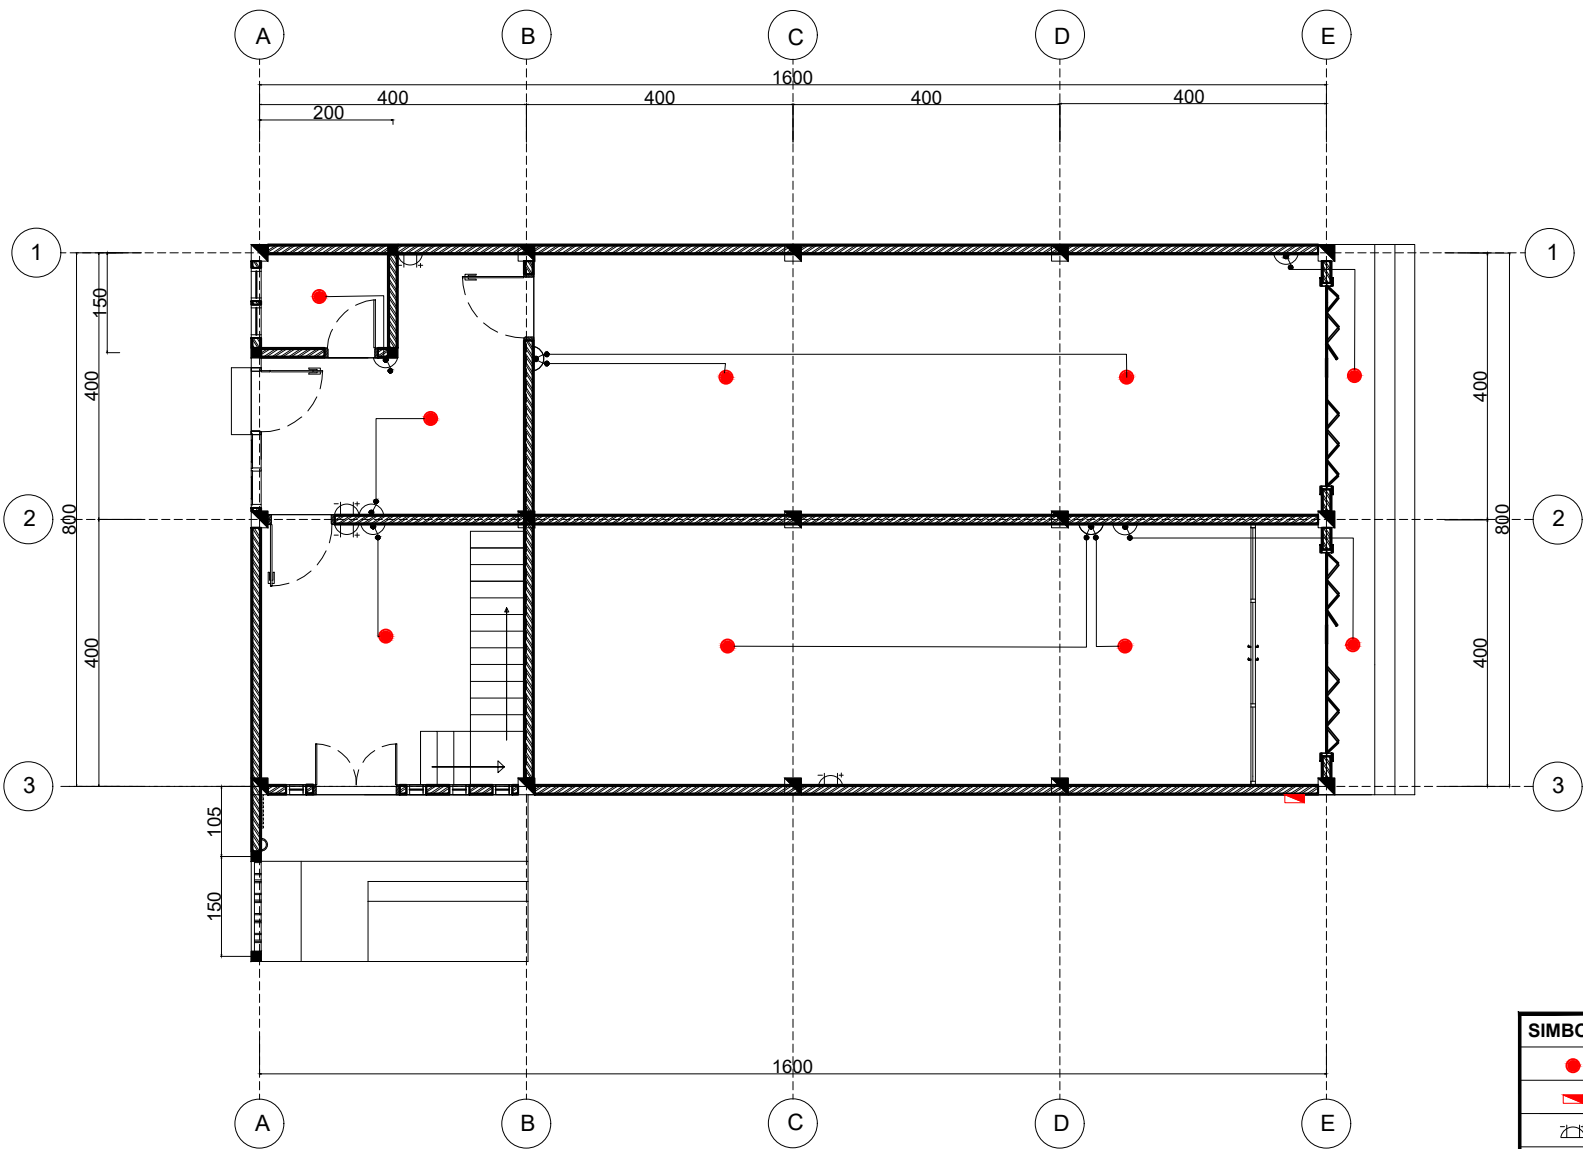

TABEL KEBUTUHAN BAHAN LISTRIK

SIMBOL	KETERANGAN	JUMLAH
●	Lampu	9 Buah
⏻	Box MCB 450 Kwh	1 Buah
⏻	Stop Kontak	4 Buah
⏻	Sakelar Tunggal	5 Buah
⏻	Sakelar Ganda	2 Buah

RENCANA INSTALASI LISTRIK LT 1
SKALA 1:100



BANGUNAN KOMERSIAL

LOKASI

Kendari, Sulawesi Tenggara

DI GAMBAR OLEH

PARAF

ATIKA, S.Ars

PEMILIK PROYEK

PARAF

AZAM


NAMA GAMBAR

GARIS SEMPADAN JALAN


1.
2.
3.
4.

SKALA

NO. LEMBAR

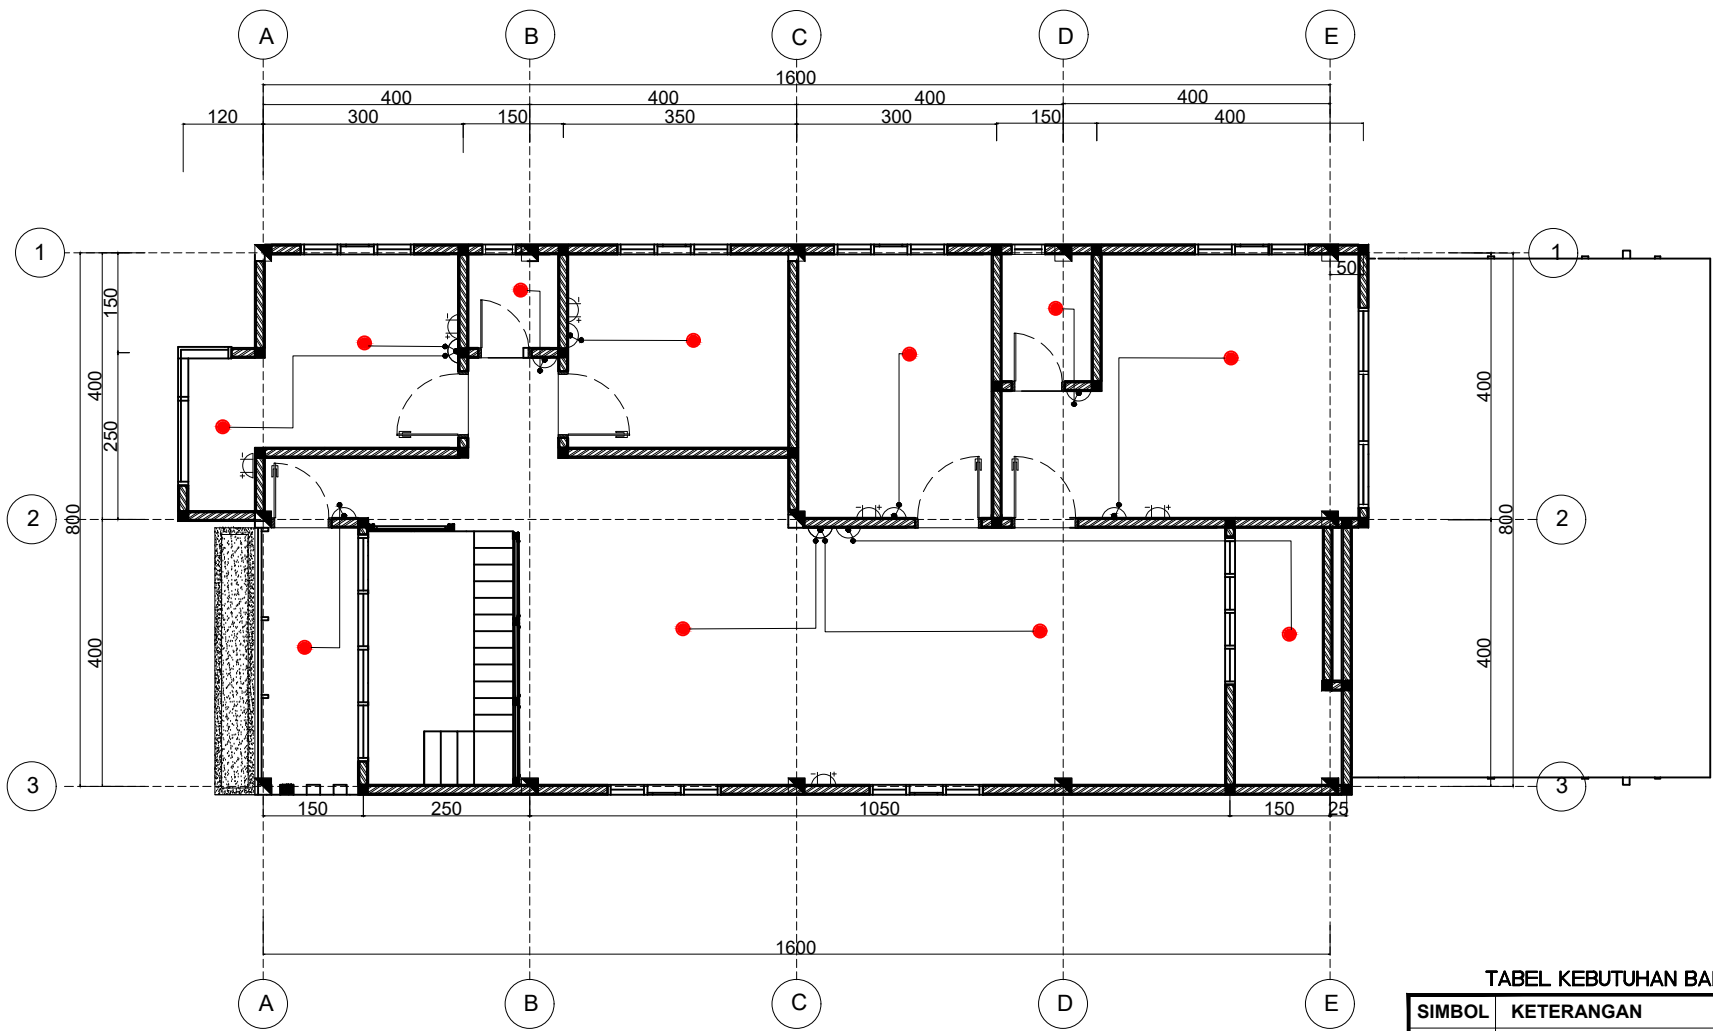

RENCANA INSTALASI LISTRIK LT 2
SKALA 1:100

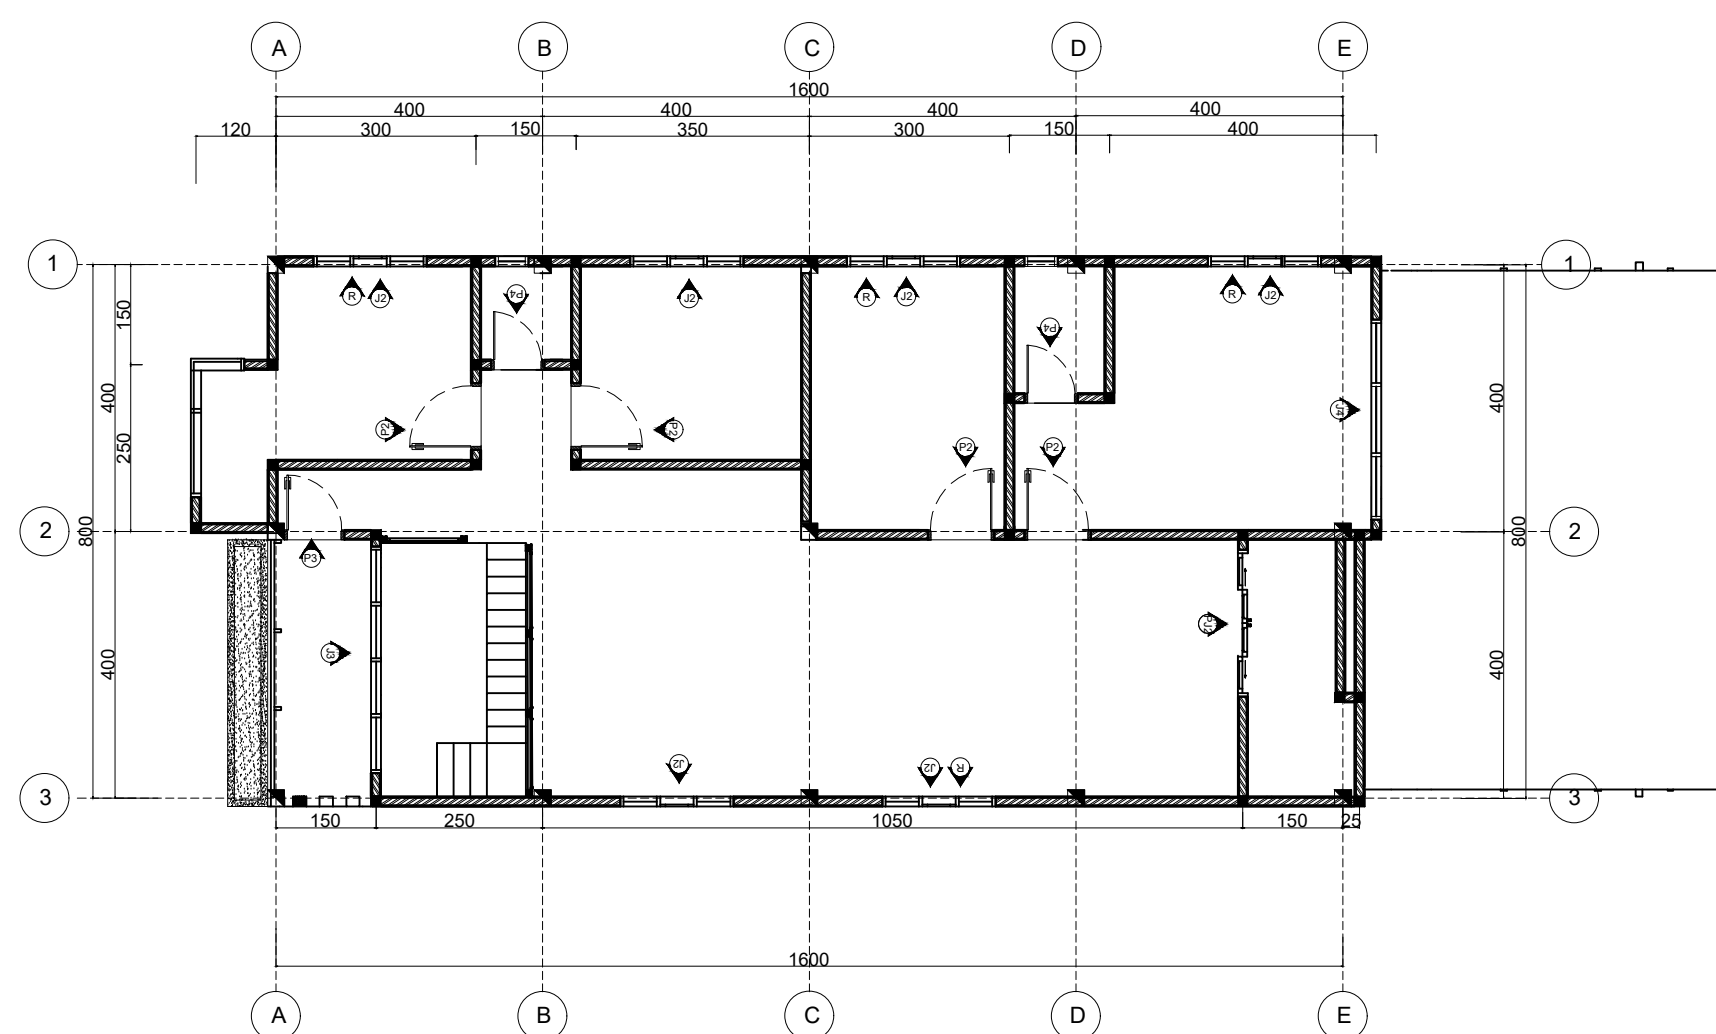

KETERANGAN	SIMBOL	JUMLAH
PINTU RUKO		0
PINTU JENDELA		0
PINTU GESER, JENDELA		1
PINTU 2 DAUN		0
PINTU 1 DAUN		4
PINTU 1 DAUN		1
PINTU WC		2
JENDELA		0
JENDELA		6
JENDELA		1
JENDELA		1
ROSTER		20

RENCANA INSTALASI LISTRIK LT 2
SKALA 1:100



BANGUNAN KOMERSIAL

LOKASI

Kendari, Sulawesi Tenggara

DI GAMBAR OLEH

PARAF

ATIKA, S.Ars

PEMILIK PROYEK

PARAF

AZAM

NAMA GAMBAR

GARIS SEMPADAN JALAN

1.	
2.	
3.	
4.	

SKALA

NO. LEMBAR



BANGUNAN KOMERSIAL

LOKASI

Kendari, Sulawesi Tenggara

DI GAMBAR OLEH

PARAF

ATIKA, S.Ars

PEMILIK PROYEK

PARAF

AZAM

NAMA GAMBAR

GARIS SEMPADAN JALAN

1.


2.

3.

4.


SKALA

NO. LEMBAR

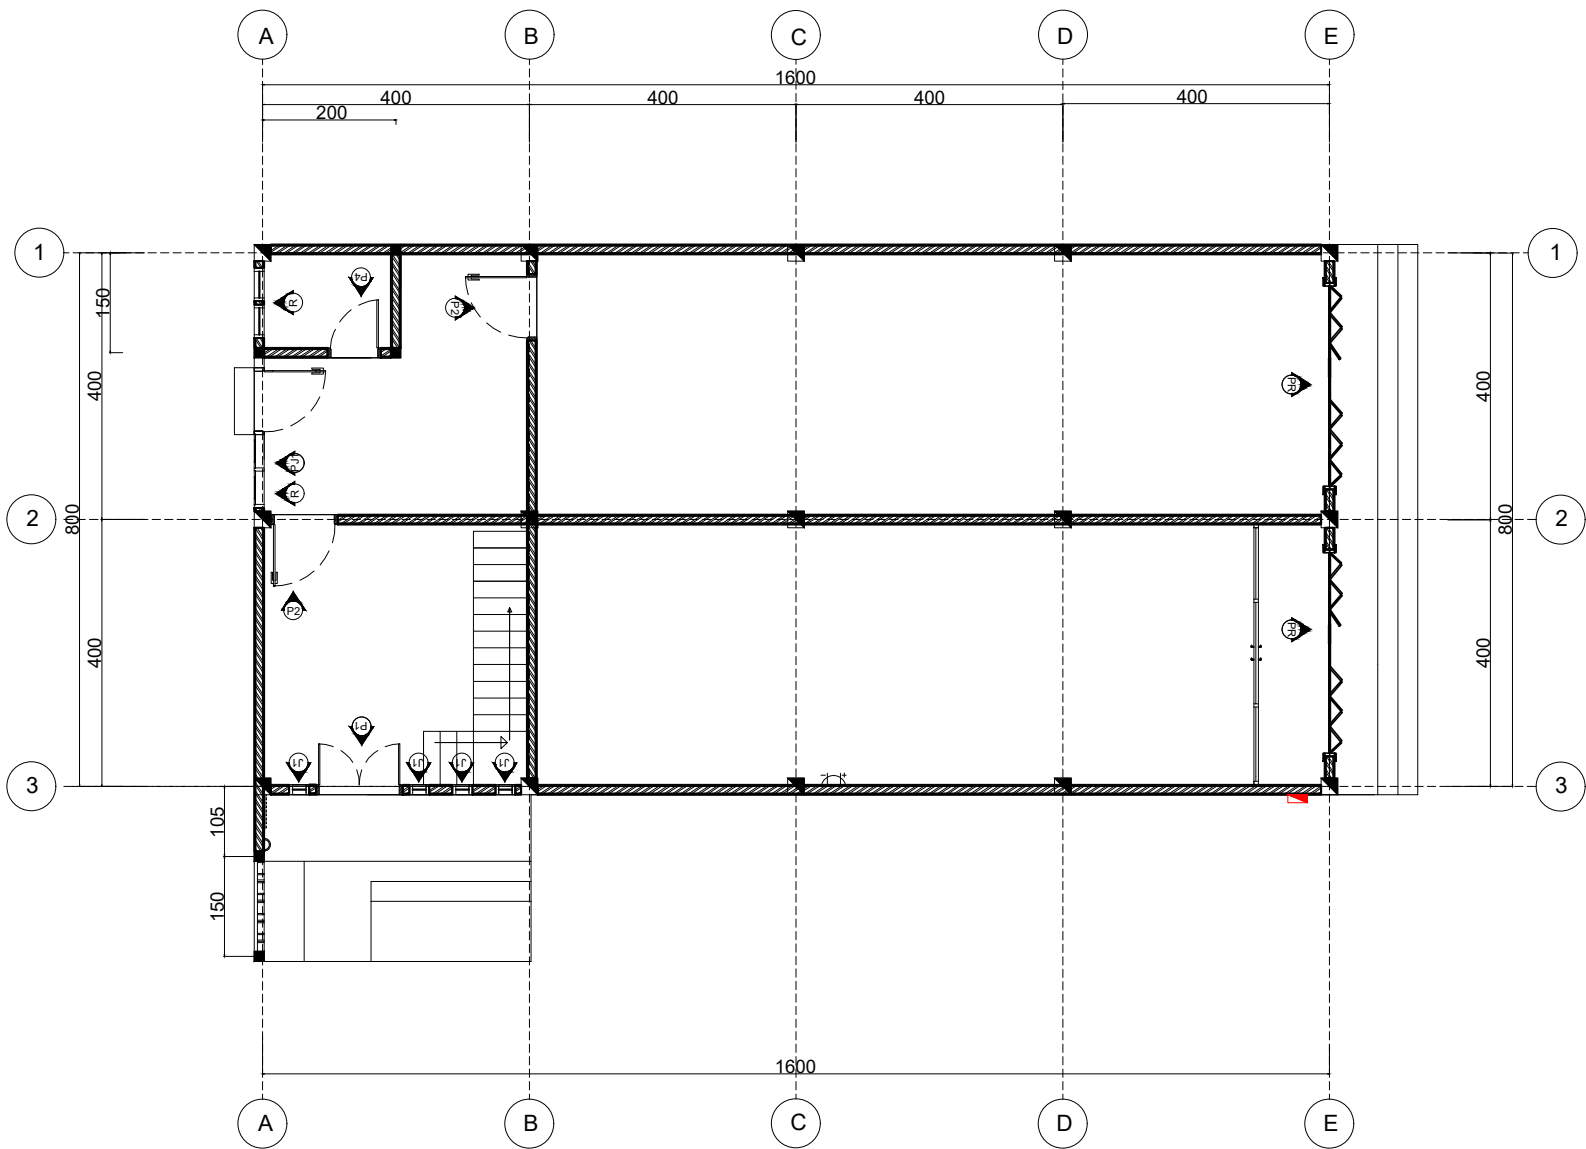


KETERANGAN	SIMBOL	JUMLAH
PINTU RUKO		2
PINTU JENDELA		1
PINTU GESER, JENDELA		0
PINTU 2 DAUN		1
PINTU 1 DAUN		2
PINTU 1 DAUN		0
PINTU WC		1
JENDELA		4
JENDELA		0
JENDELA		0
JENDELA		0
ROSTER		4

RENCANA INSTALASI LISTRIK LT 1
SKALA 1:100

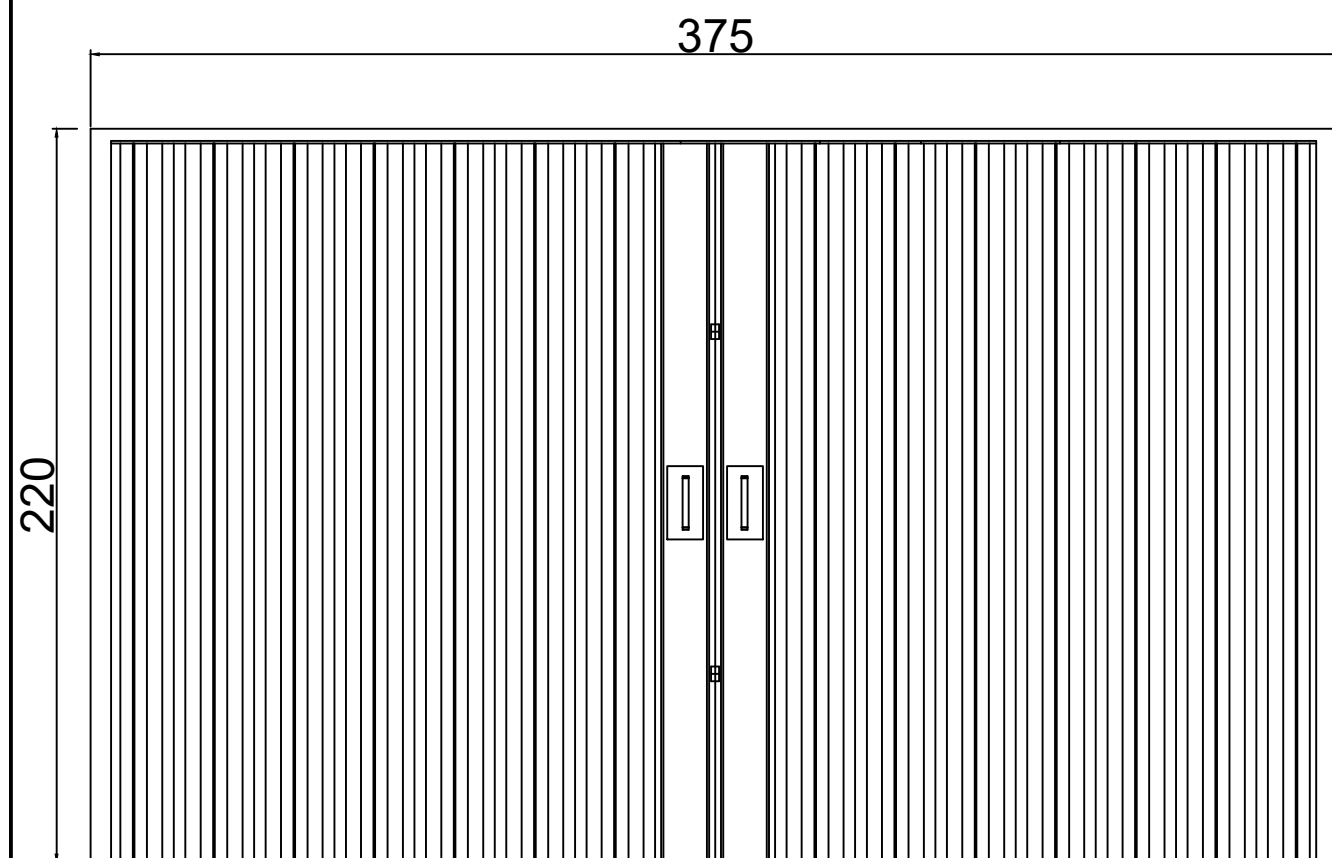

PINTU RUKO (2 buah)
SKALA 1:20

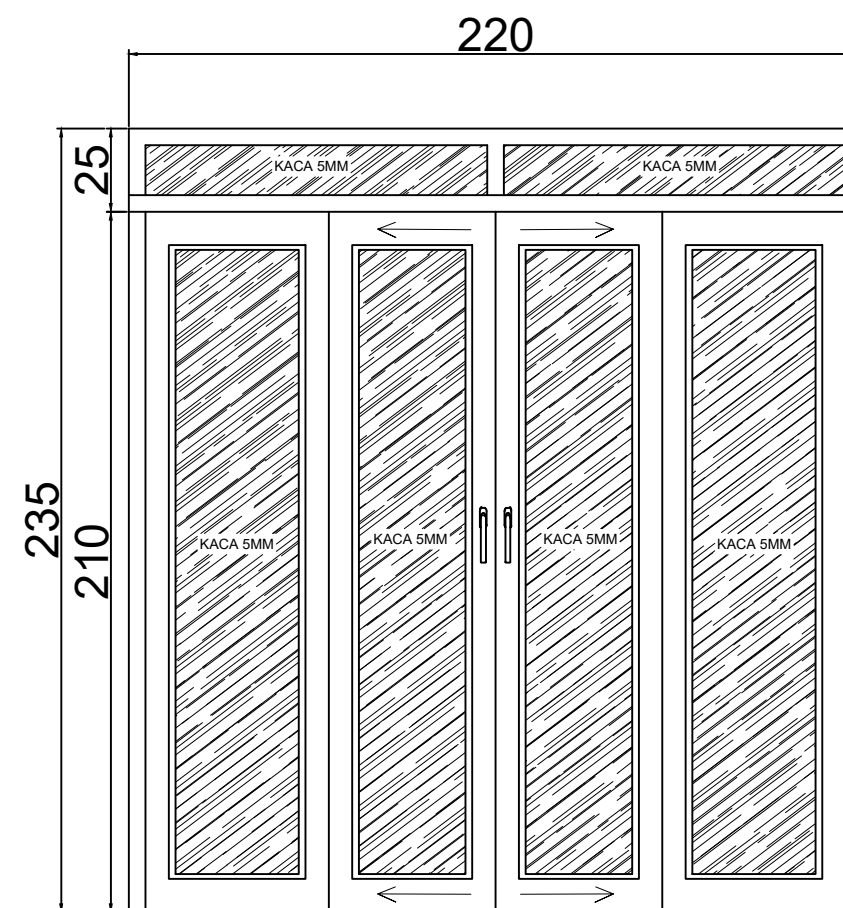

PJ2 (1 BUAH)
SKALA 1:20



BANGUNAN KOMERSIAL

LOKASI

Kendari, Sulawesi Tenggara

DI GAMBAR OLEH

PARAF

ATIKA, S.Ars

PEMILIK PROYEK

PARAF

AZAM



NAMA GAMBAR

GARIS SEMPADAN JALAN



- 1.
- 2.
- 3.
- 4.

SKALA



NO. LEMBAR

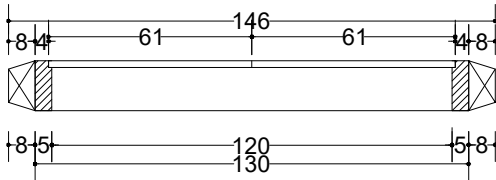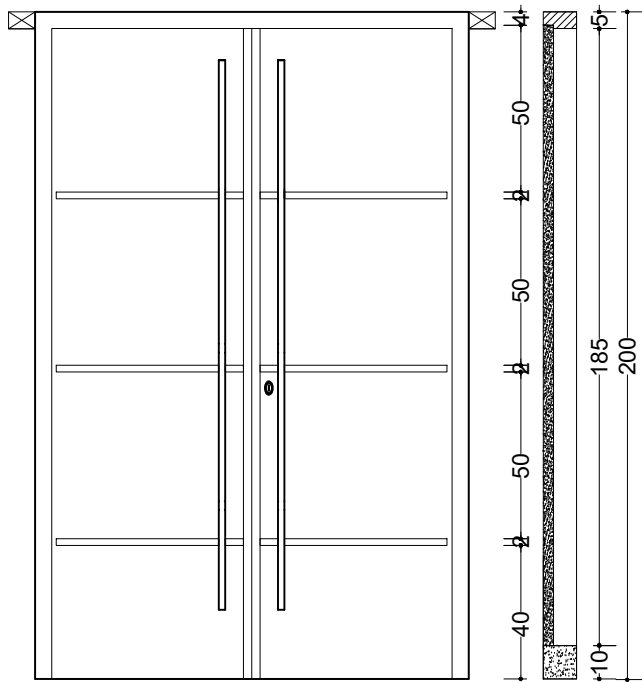


P1 (1 BUAH)
SKALA 1:20

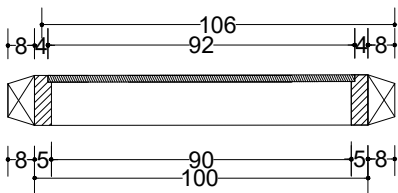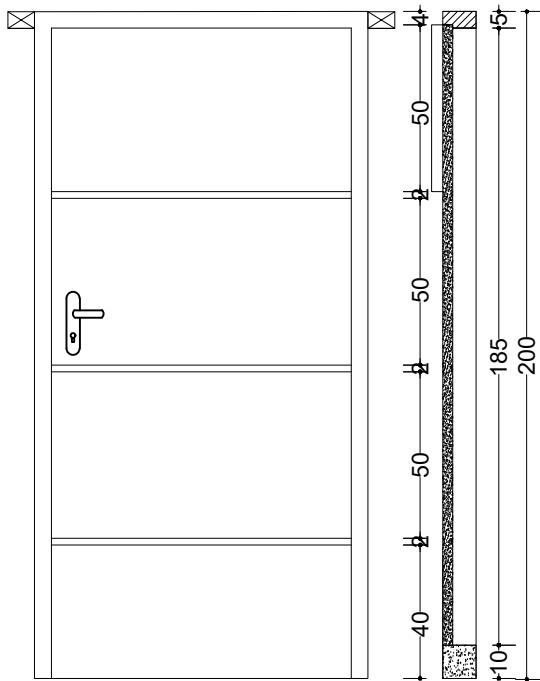

P2 (6 BUAH)
SKALA 1:20

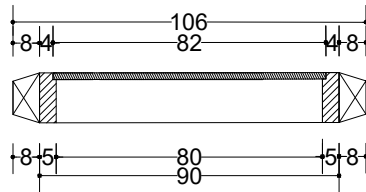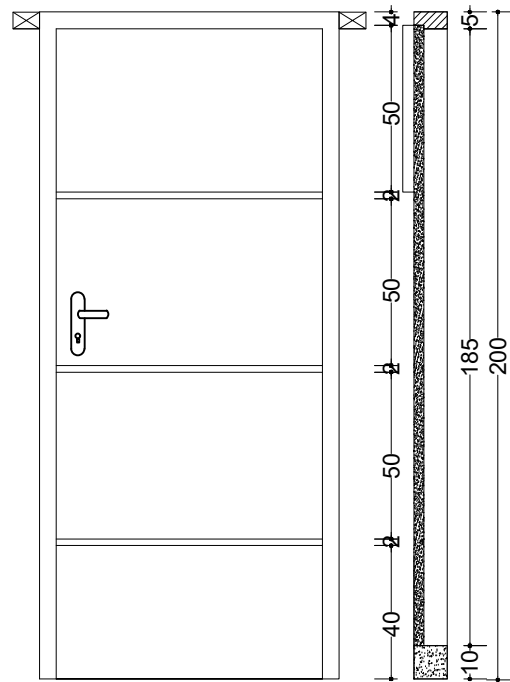

P3 (1 BUAH)
SKALA 1:20

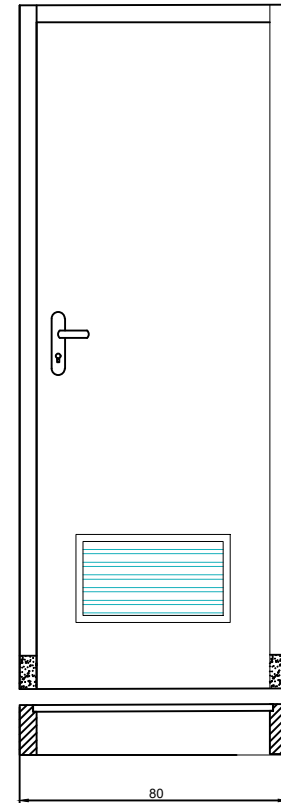

P4 (3 BUAH)
SKALA 1:20



BANGUNAN KOMERSIAL

LOKASI

Kendari, Sulawesi Tenggara

DI GAMBAR OLEH

PARAF

ATIKA, S.Ars

PEMILIK PROYEK

PARAF

AZAM


NAMA GAMBAR

GARIS SEMPADAN JALAN

1.	
2.	
3.	
4.	

SKALA

NO. LEMBAR

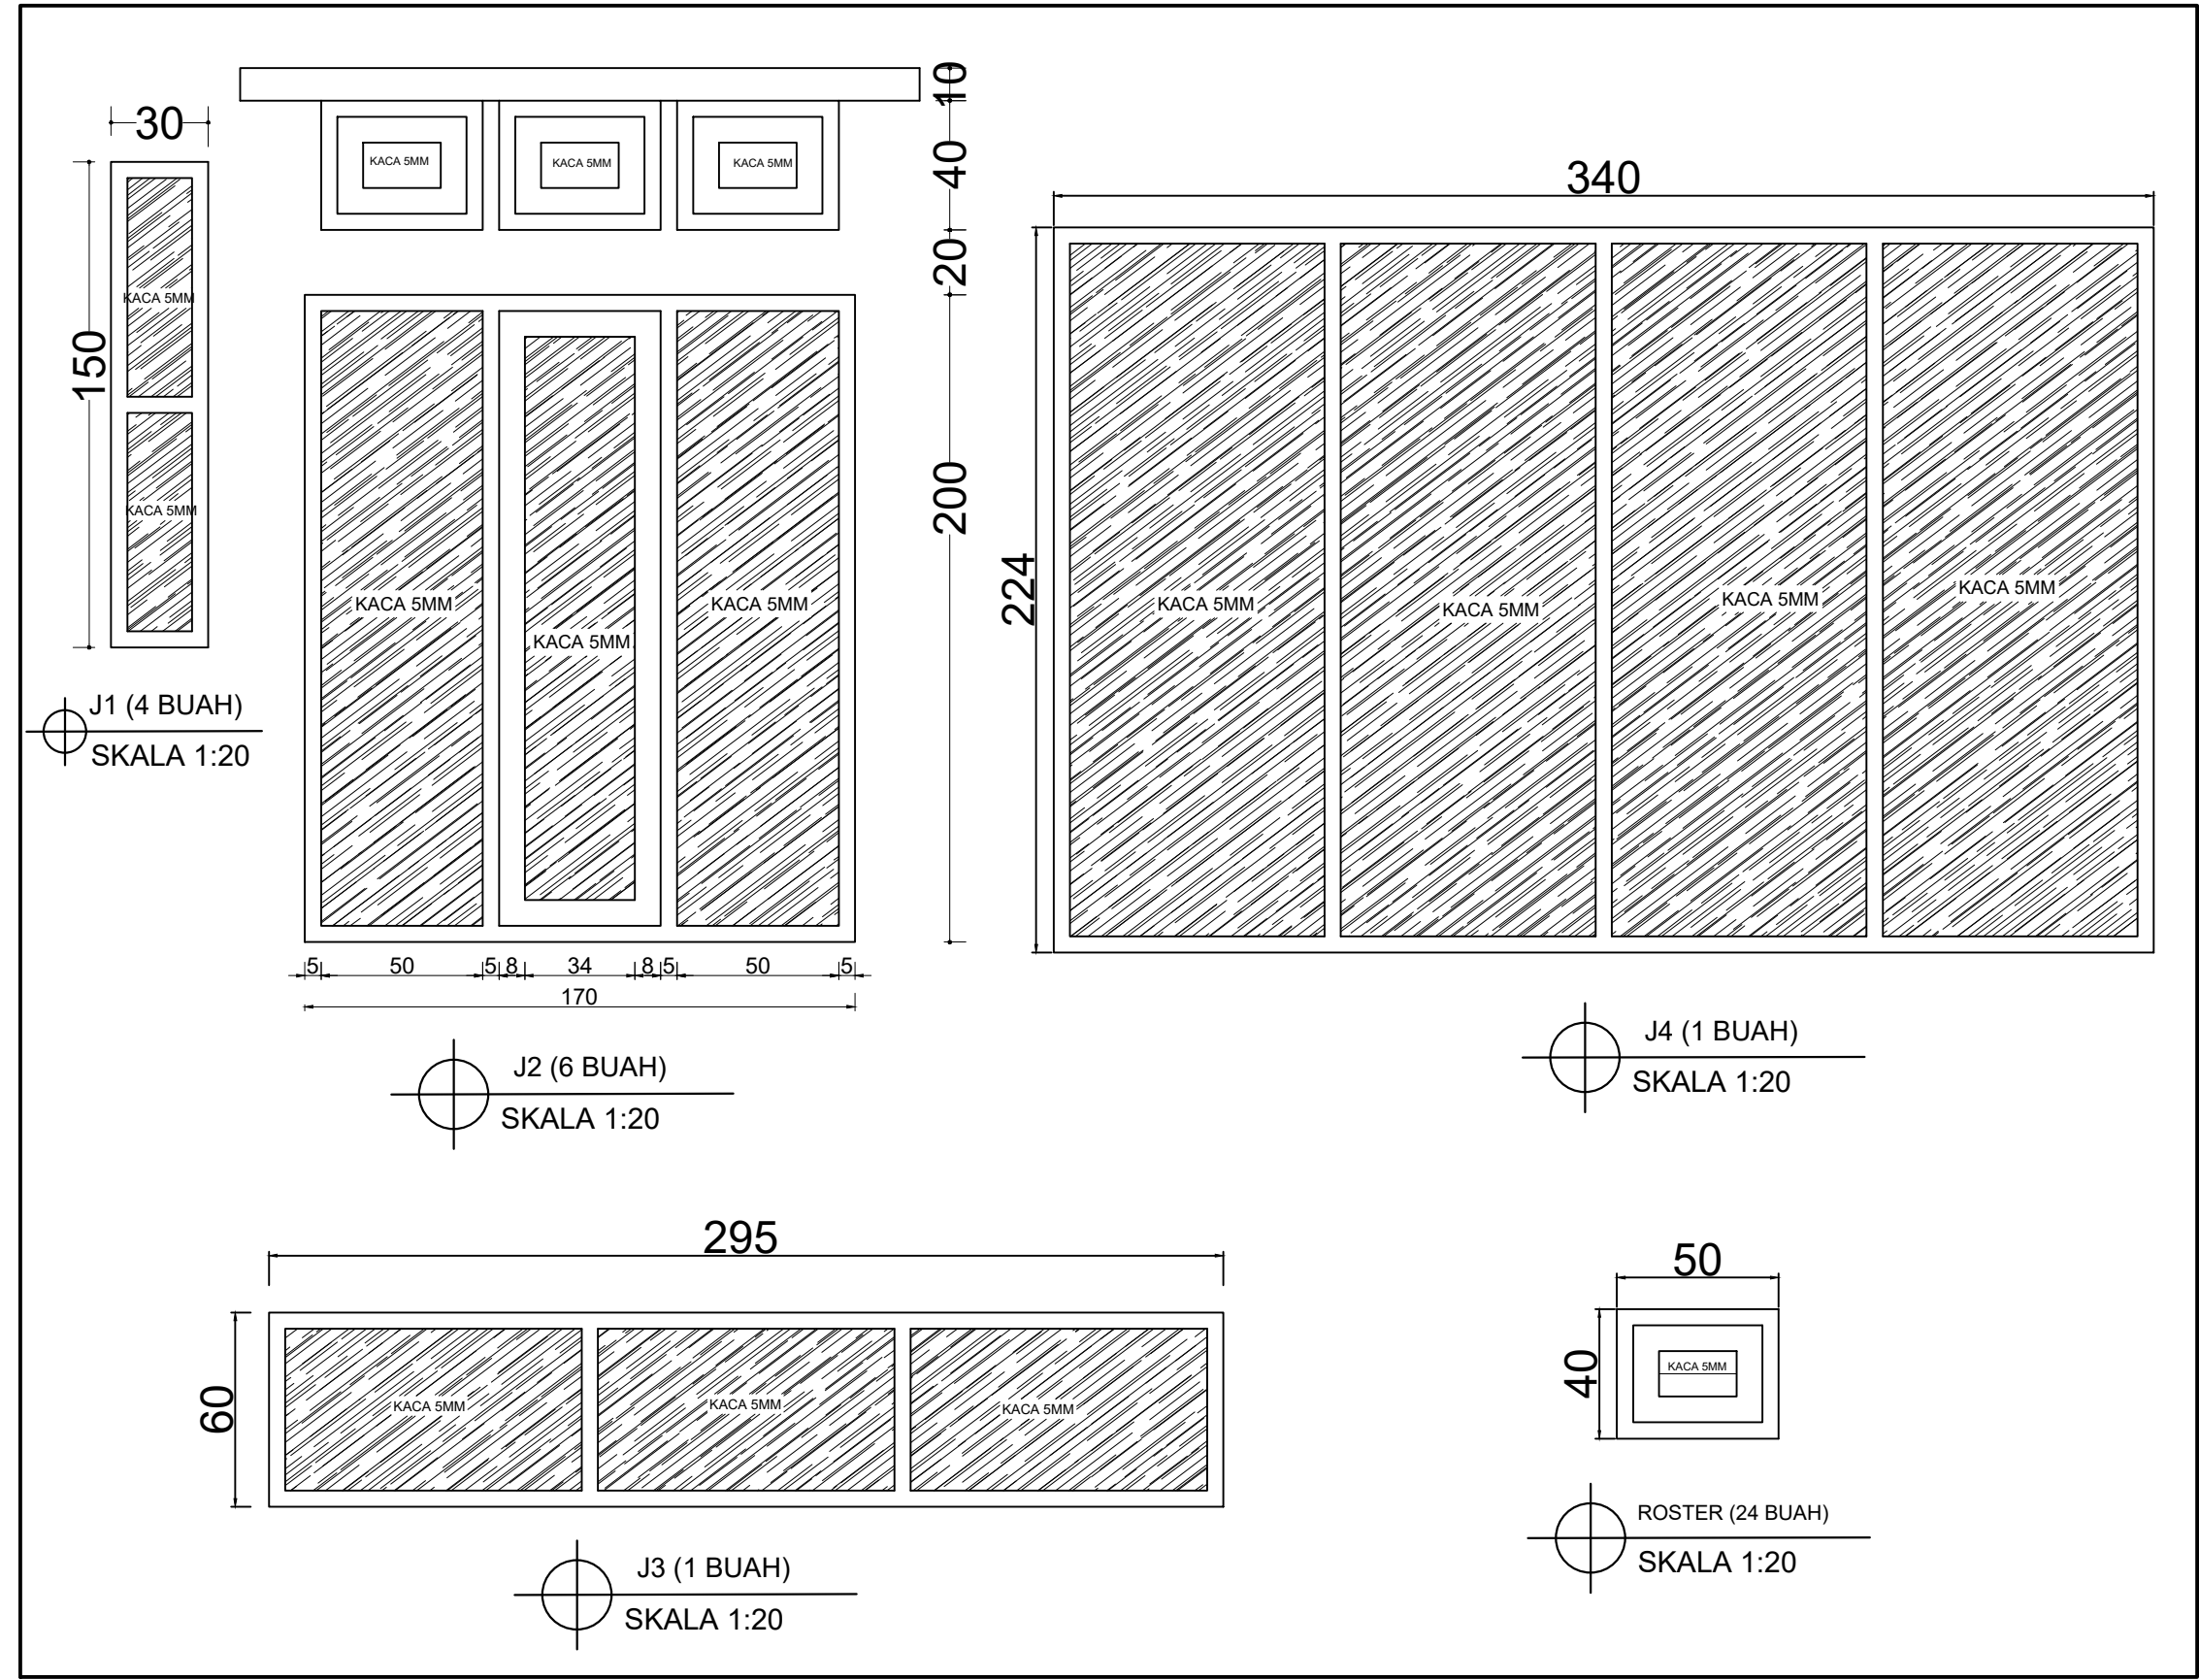

BANGUNAN KOMERSIAL

LOKASI

Kendari, Sulawesi Tenggara

DI GAMBAR OLEH PARAF

ATIKA, S.Ars

PEMILIK PROYEK PARAF

AZAM

NAMA GAMBAR

GARIS SEMPADAN JALAN

- | | |
|----|--|
| 1. | |
| 2. | |
| 3. | |
| 4. | |

SKALA NO. LEMBAR



BANGUNAN KOMERSIAL

LOKASI

Kendari, Sulawesi Tenggara

DI GAMBAR OLEH

PARAF

ATIKA, S.Ars

PEMILIK PROYEK

PARAF

AZAM


NAMA GAMBAR

GARIS SEMPADAN JALAN


- | | |
|----|--|
| 1. | |
| 2. | |
| 3. | |
| 4. | |

SKALA

NO. LEMBAR

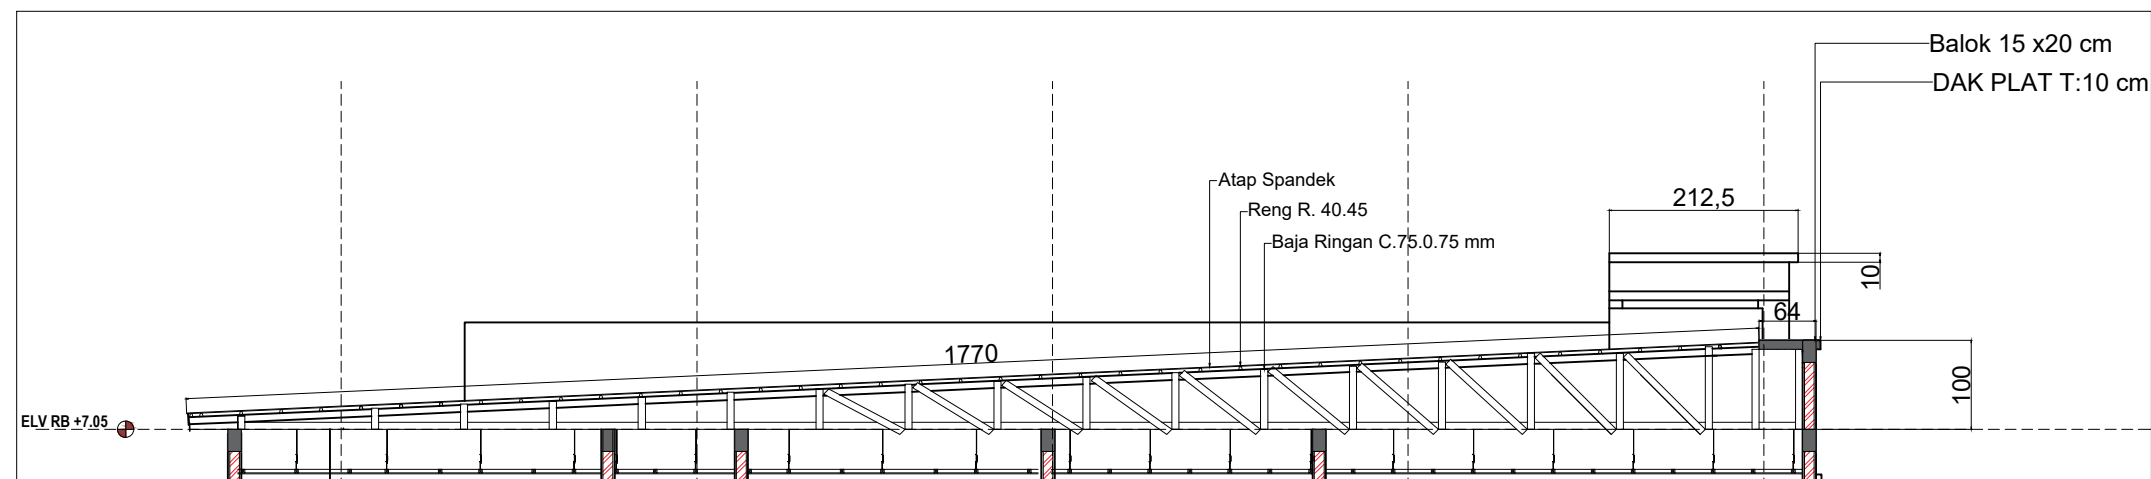

DETAIL POTONGAN ATAP A - A
SKALA 1:75

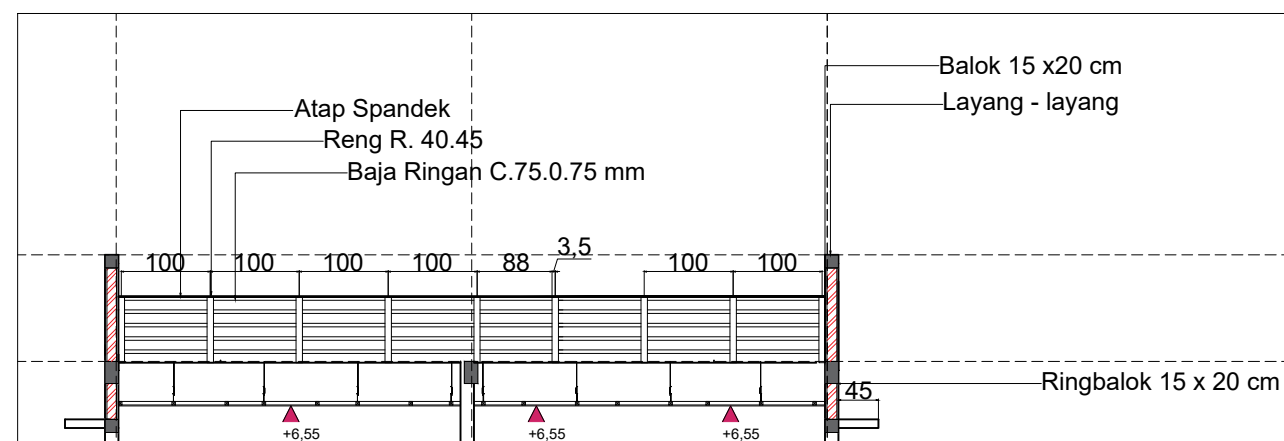

DETAIL POTONGAN ATAP B - B
SKALA 1:75